



MARNISSI EYA


CHARGE D'ETUDE
ÉLECTRICITÉ



-01- A PROPOS MOI	-02- MON EXPERIENCE	-03- DOMAINE D'EXPERTISE	-04- MON TRAVAIL
			





A PROPOS MOI

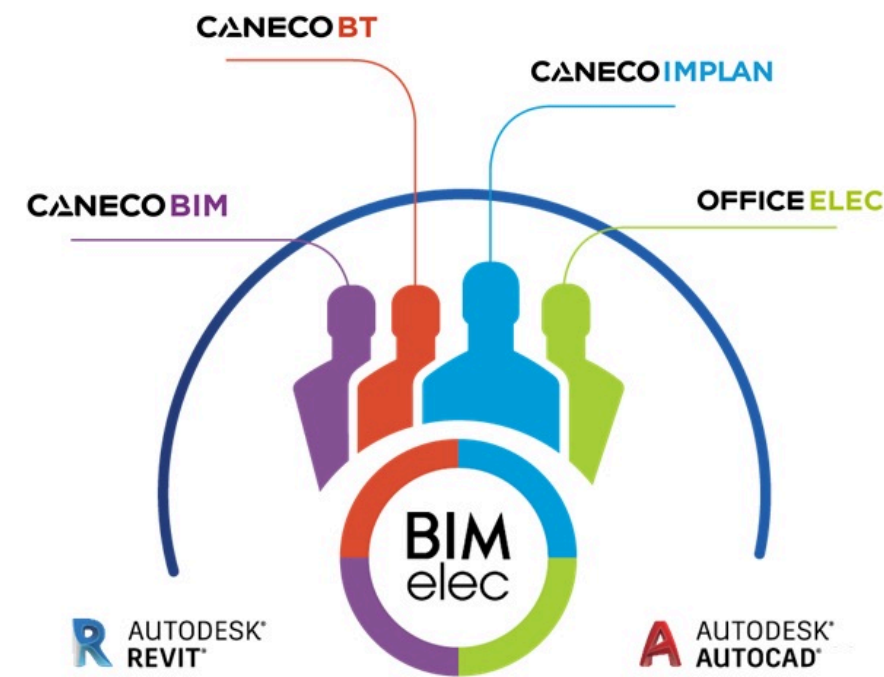

Je suis une modeleuse Bim spécialisée en CFO/CFA électrique, avec trois années d'expérience enrichissante dans le domaine des bureaux d'études. Passionné par la conception et la modélisation de systèmes électriques pour des projets de construction variés, j'ai développé une expertise solide dans l'utilisation de logiciels BIM pour optimiser la planification et la coordination des installations électriques.

Mon parcours professionnel m'a permis de participer activement à des études de projets et de contribuer à leur modélisation, démontrant ainsi ma capacité à fournir des solutions précises et efficaces. Doté d'un esprit analytique et d'un engagement envers l'excellence,

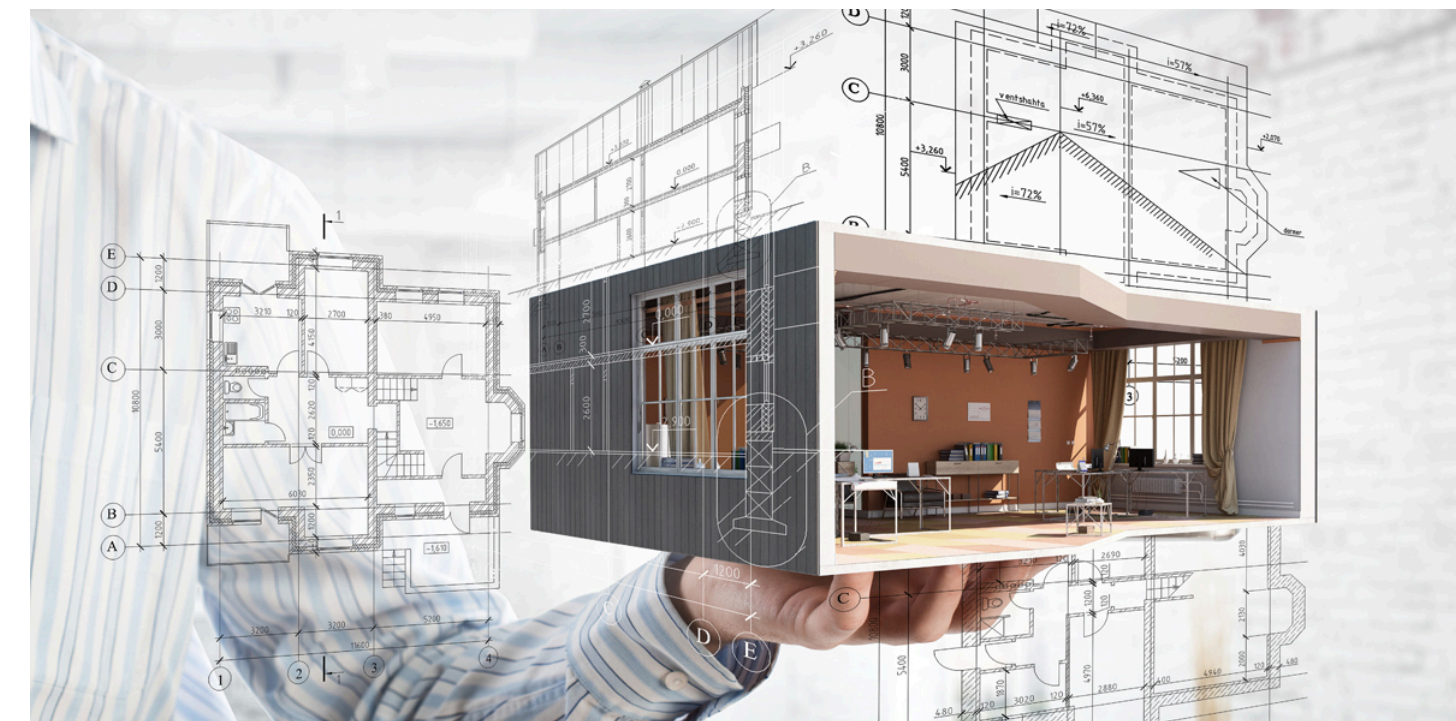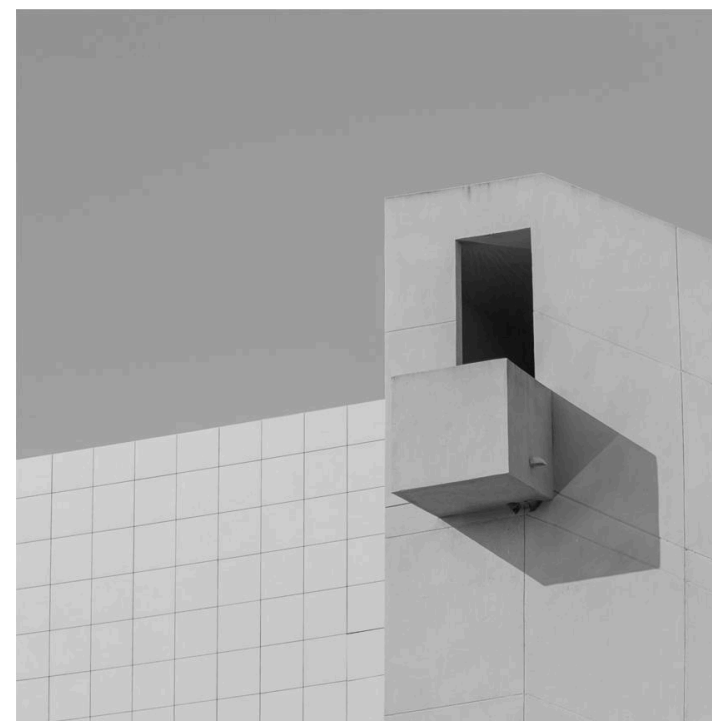



Marnissi eya

MON PROFILE

Modeleuse BIM spécialisé en CFO/CFA électrique, avec 3 ans d'expérience dans le domaine des bureaux d'études. Au cours de mon parcours, j'ai eu l'opportunité de réaliser des études de projets et de les modéliser.

MON EXPERIENCE

EDUCATION

- 2023-2025 ISEFEC | Master professionnel en Enelectrotechnique et Energies Renouvelables
- 2017-2020 ISET BIZERTE | Licence Appliquée en Génie Electrique
- 2015-2016 LYCEE FARHAT HACHED | Baccalauréat Science Technique

EXPERIENCE


- 2022-jusqu'a present Mosaïque engenieirie | BIM MODELEUSE
- 2021-2022 CES-Contracting engineering services | Dessinatrice projeteuse

CONTACT

Email : eaya.marnissi@gmail.com

Watshapp :+216 28584246

linkedin :www.linkedin.com/in/marnissi-eya-34b6781b9/

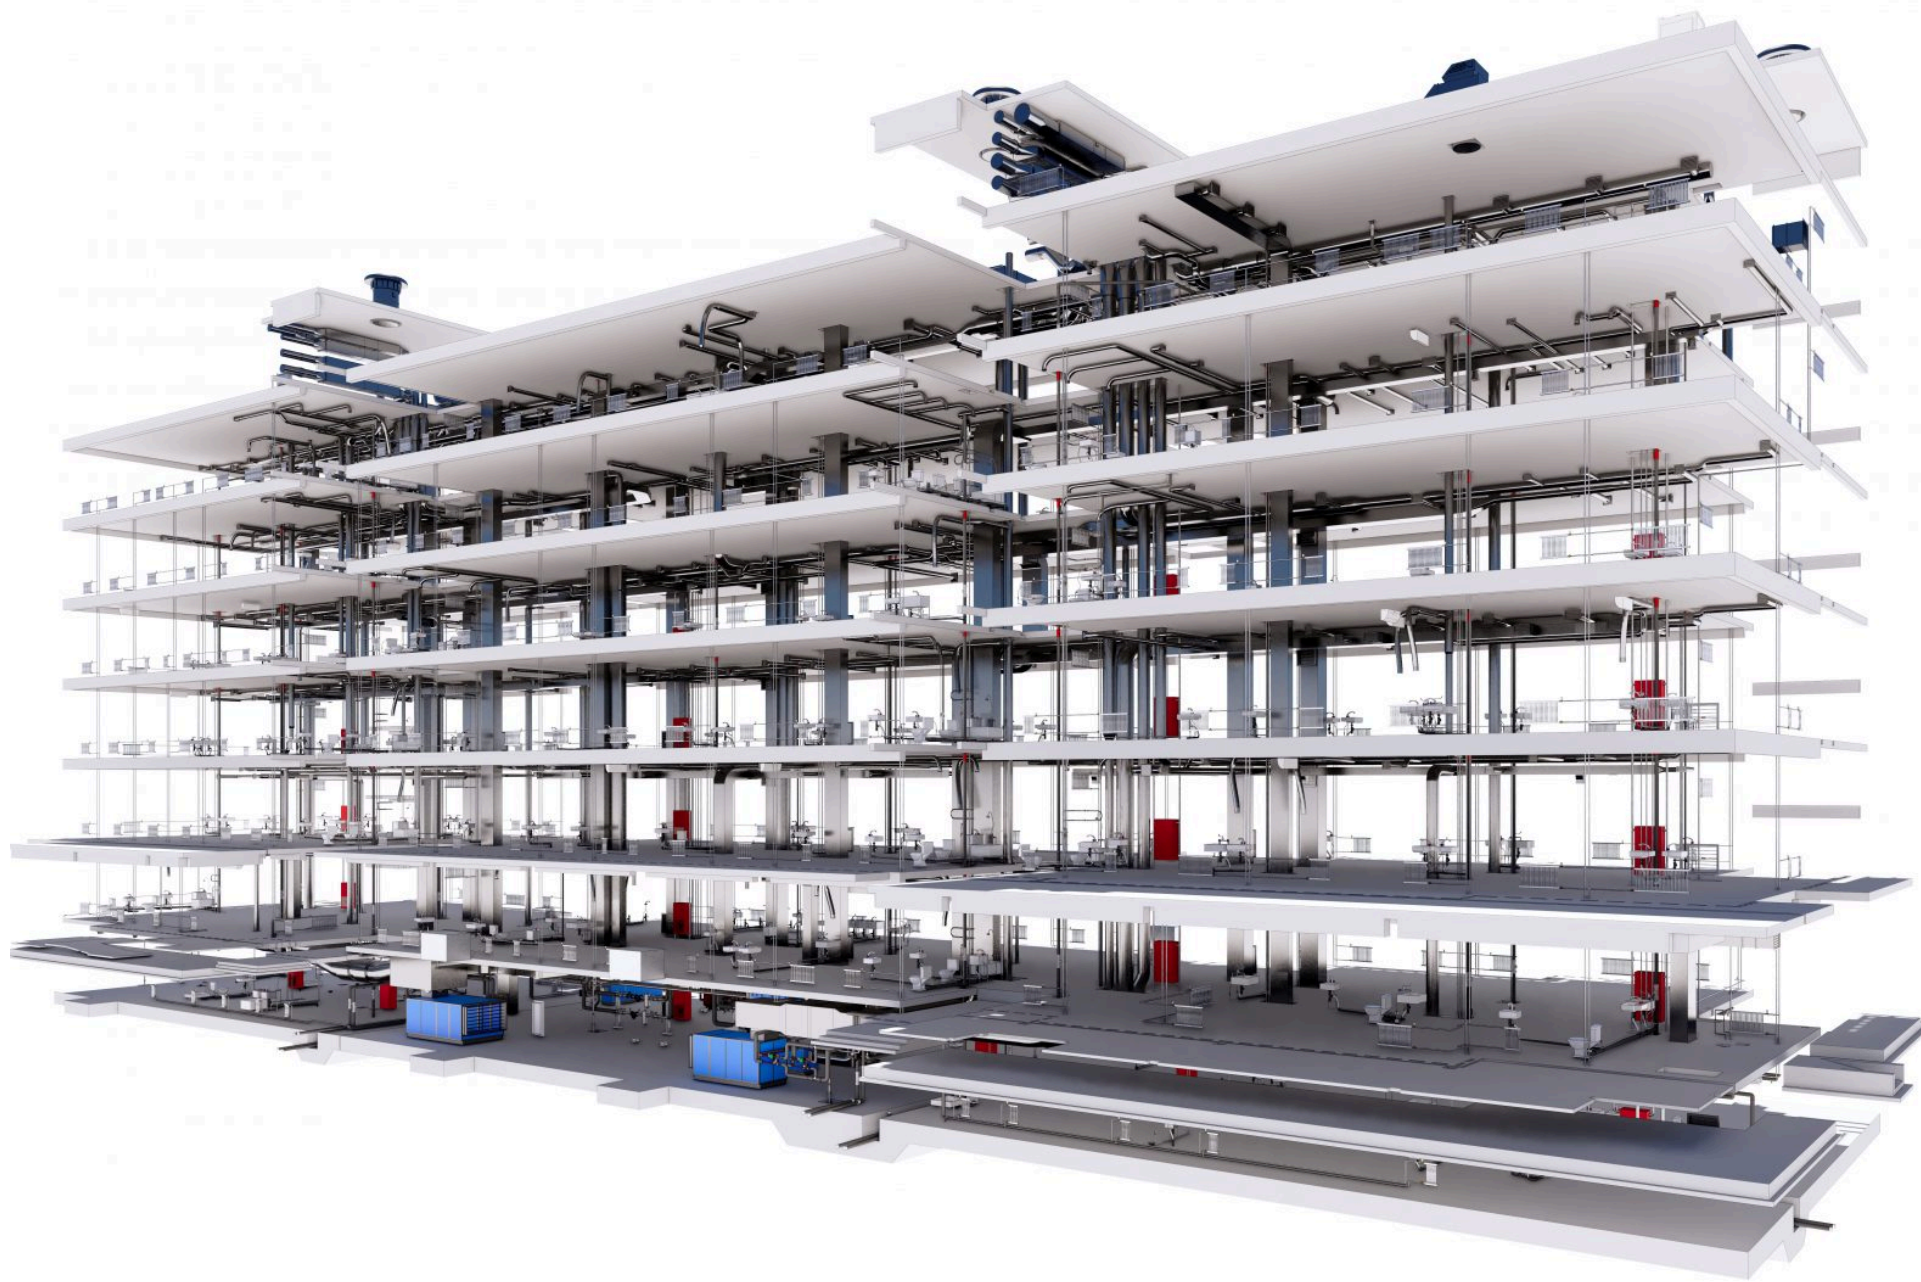

DOMAINE D'EXPERTISE

- Modélisation les équipements électriques et chemin de cable 3D.
- Réalisation des schémas synoptiques CFO/CFA/SDI.
- Réalisation des plans mise a la terre et paratonnerre .
- Réalisation note de calcul d'éclairement .
- Réalisation note de calcul basse tension et bilan de puissance.
- Réalisation des métrés (quantitatif) et chiffrages .
- Realisation plan d'exécution CFO/CFA
- Coordination avec les autres los (fluide-structure).

LOGICIELS



REVIT



AutoCAD

AUTOCAD 2D



DIALux evo

DIALUX-EVO



NAVISWORKS



CANECO-BT





CANECO-BIM




CANECO-BT



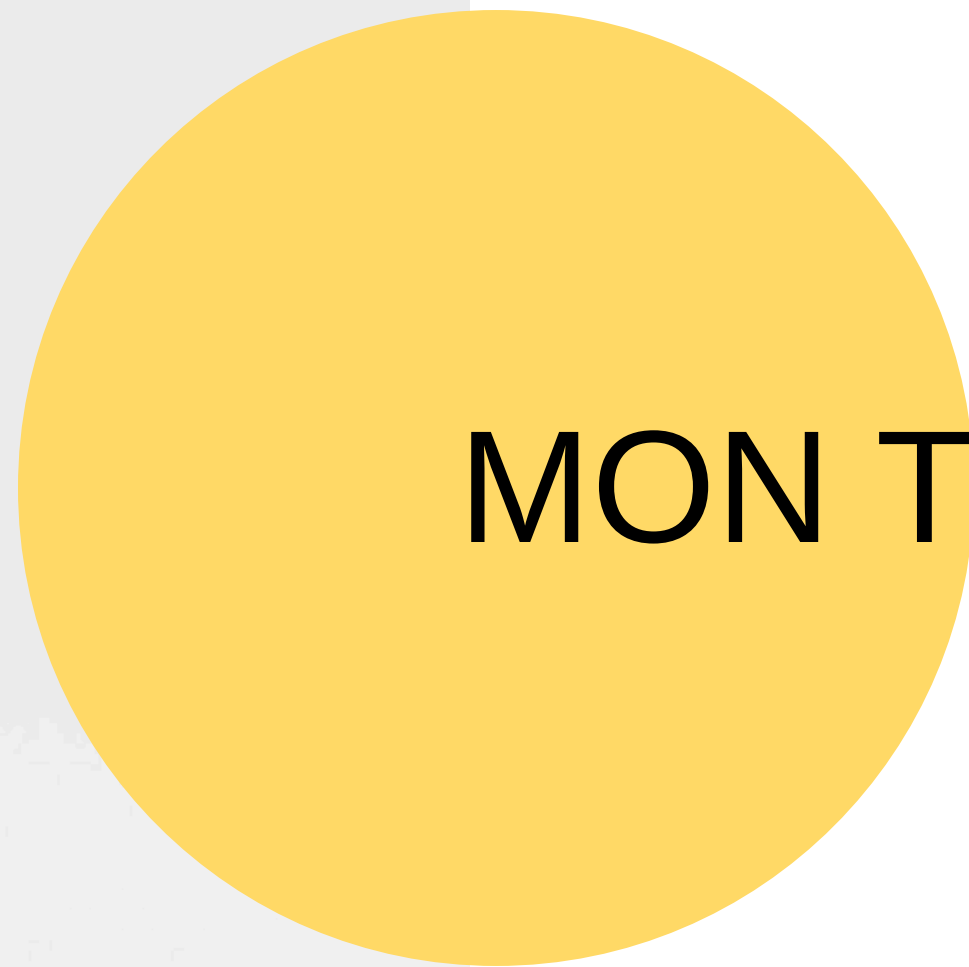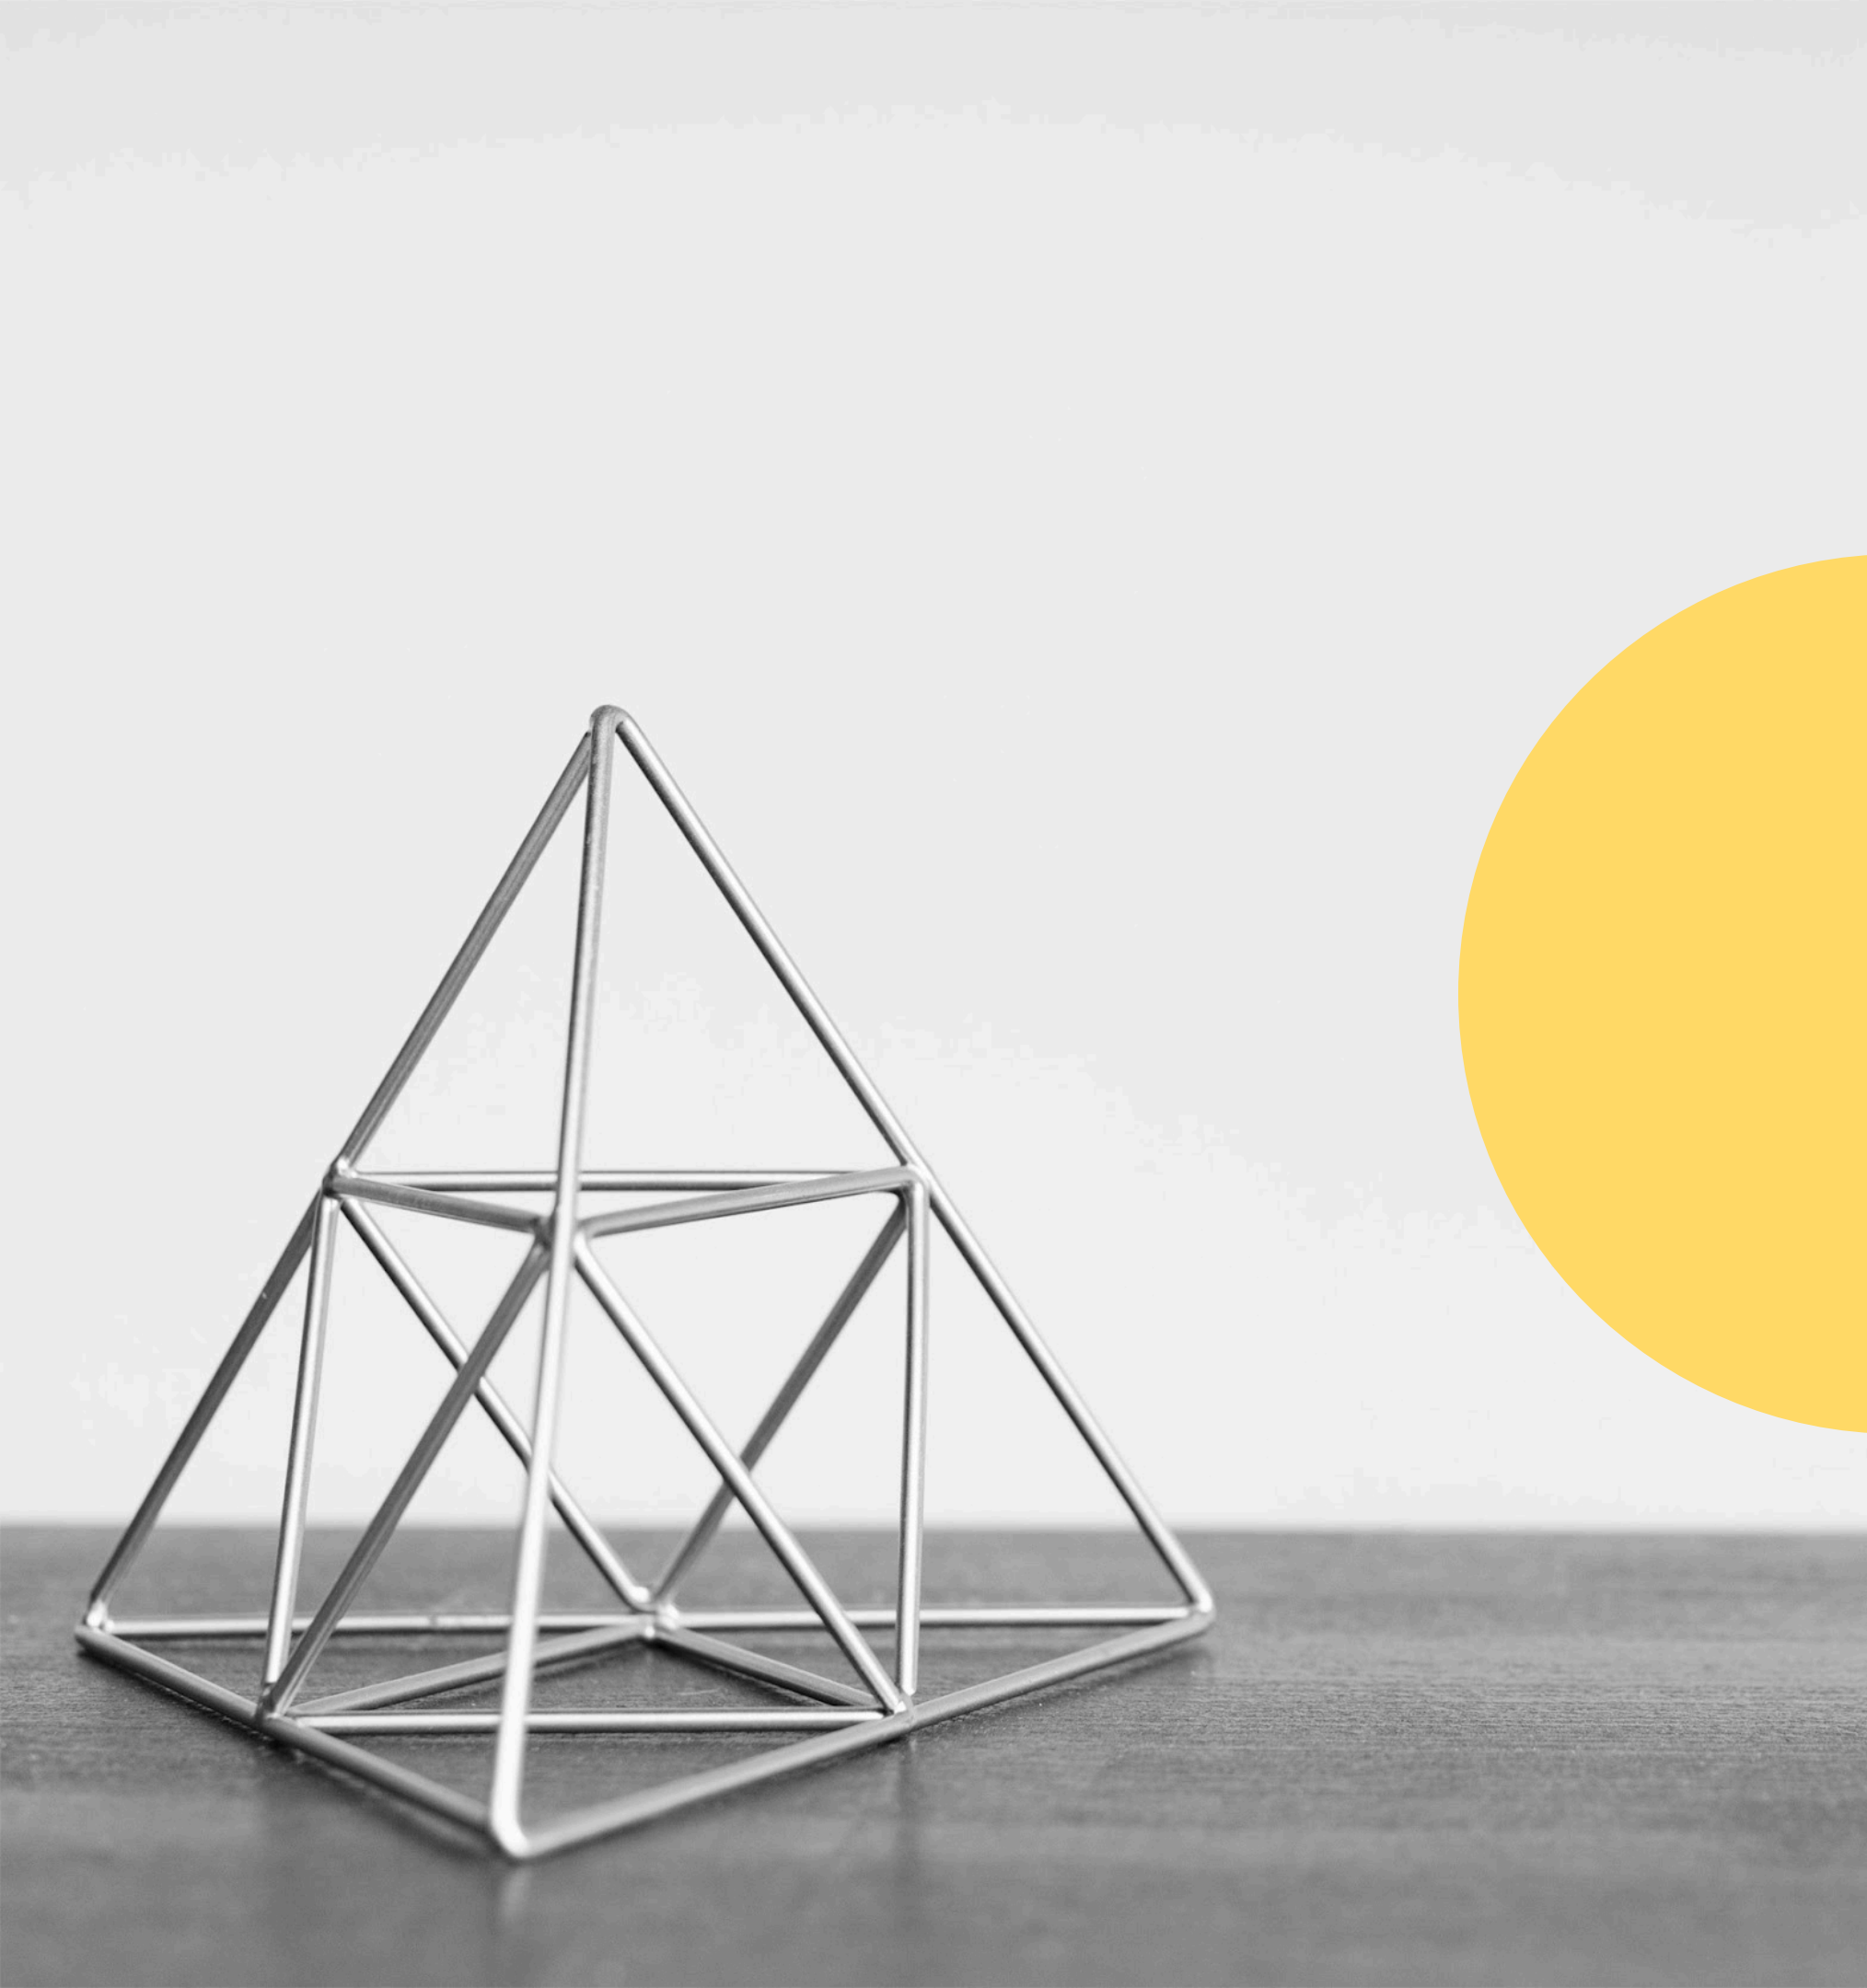


MON TRAVAIL


PROJET 1

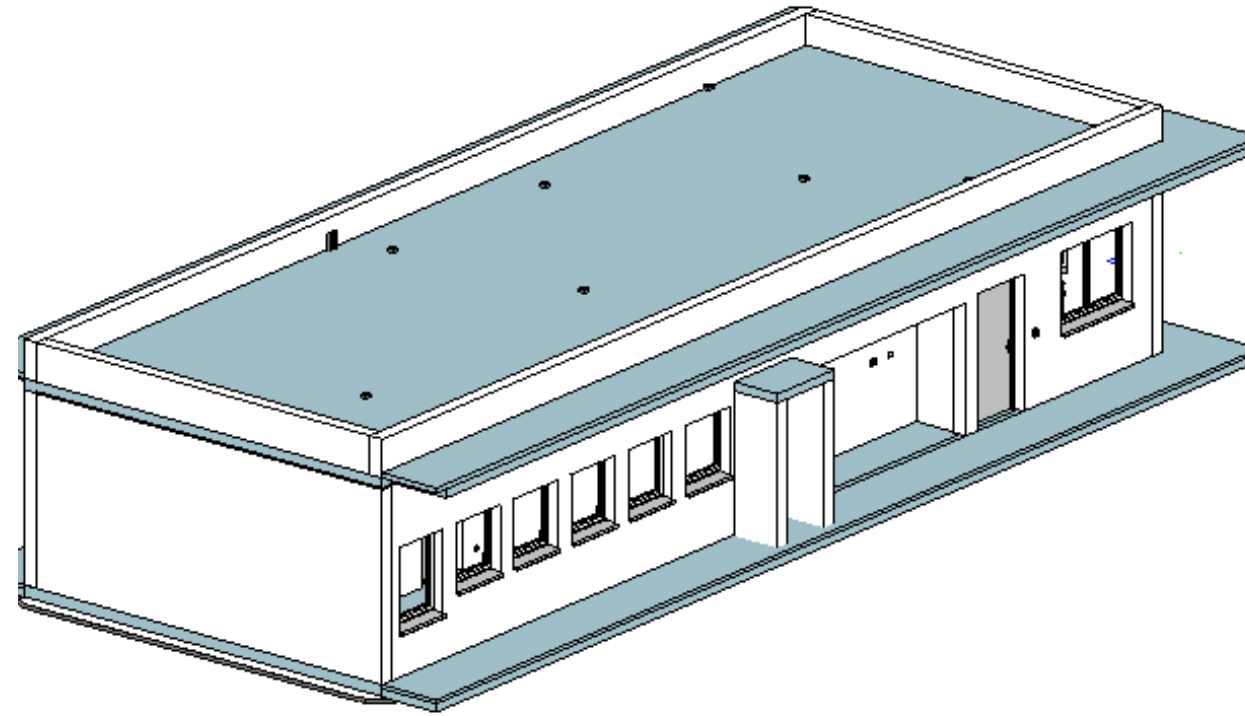


Le projet concerne la construction des gares
et des bâtiments électriques du futur métro .
Le présent descriptif a pour objet la définition
des travaux et fournitures du lot :
ELECTRICITE - COURANTS FORTS ET
COURANTS FAIBLES

PROJECT 1

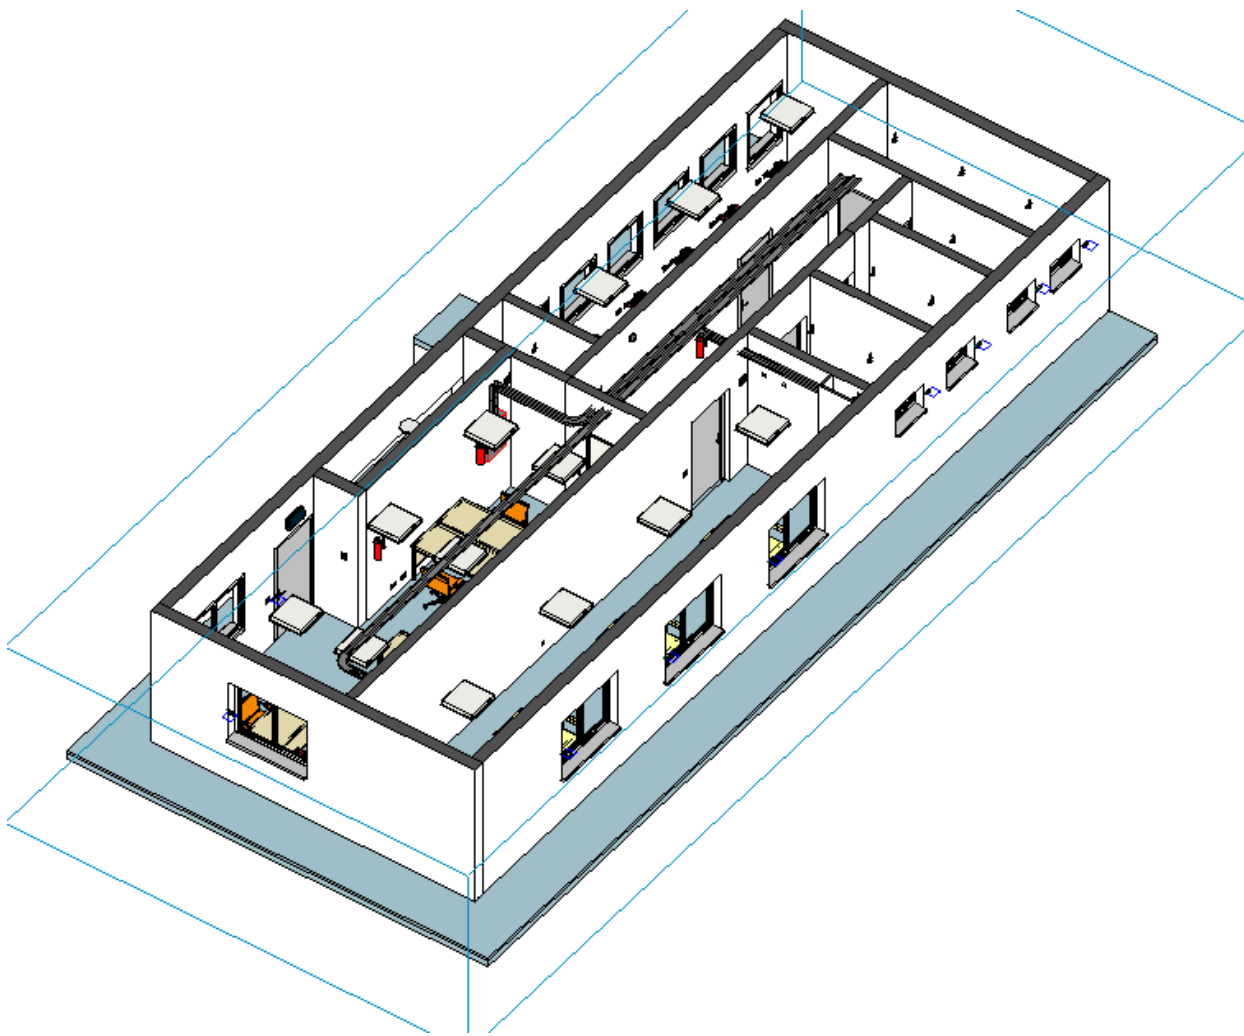

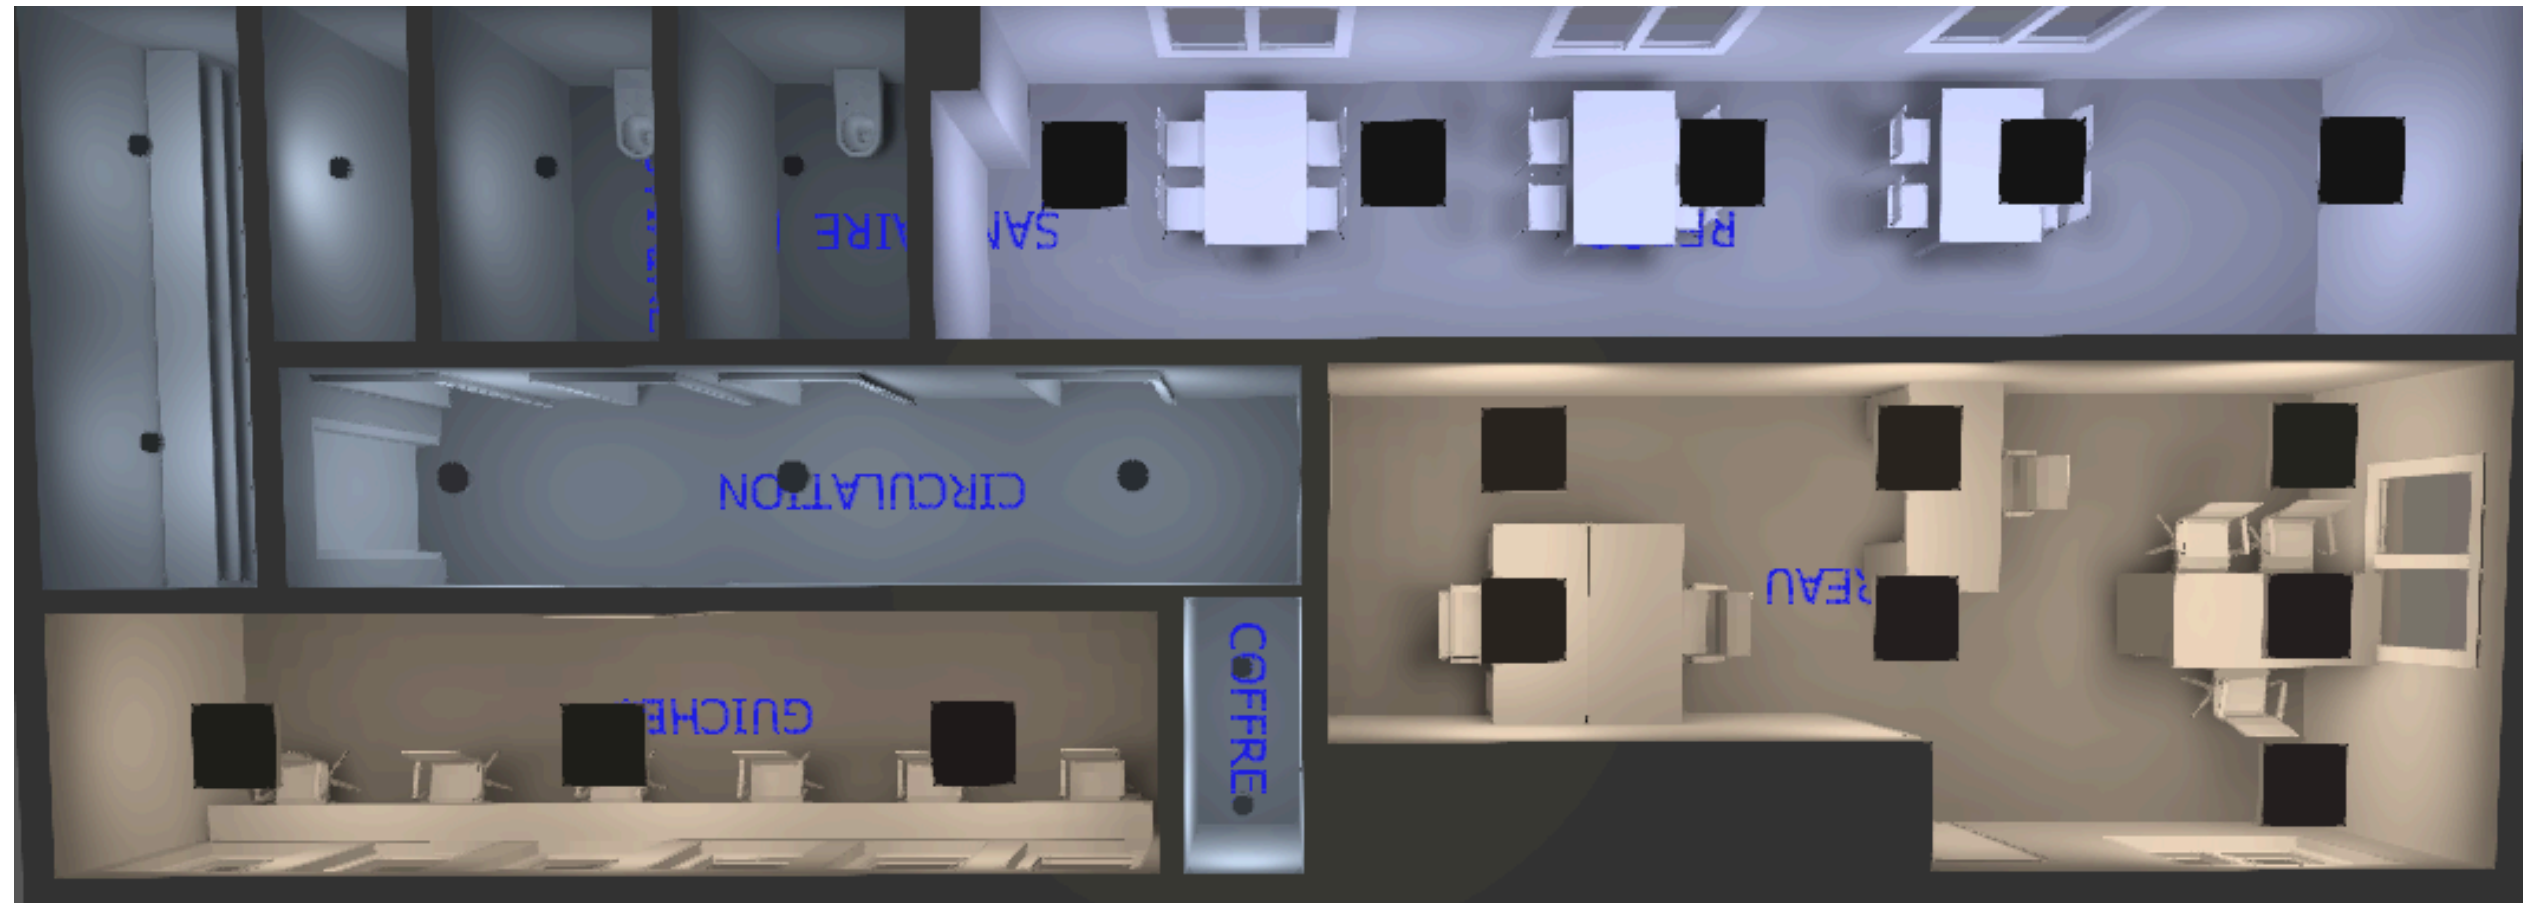


PLAN D'ETAGE

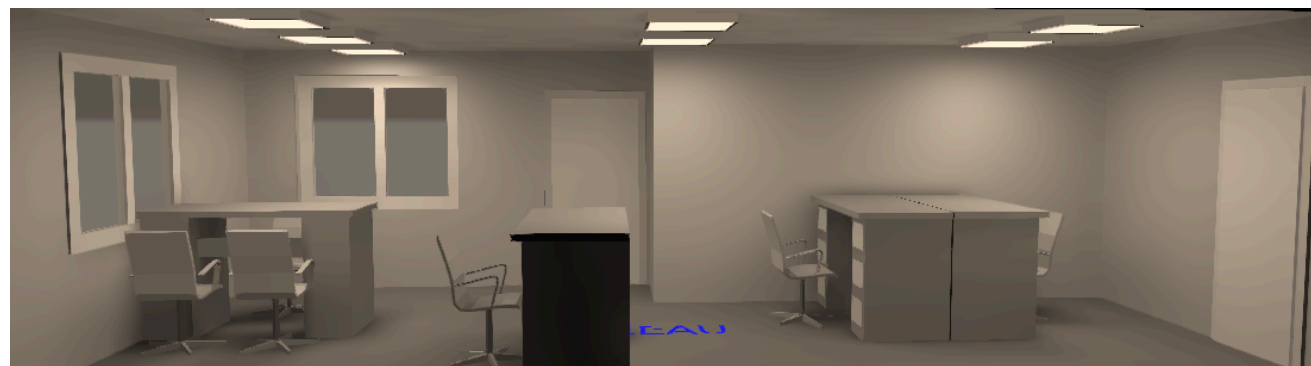


BUREAU




SALLE DE REPOS

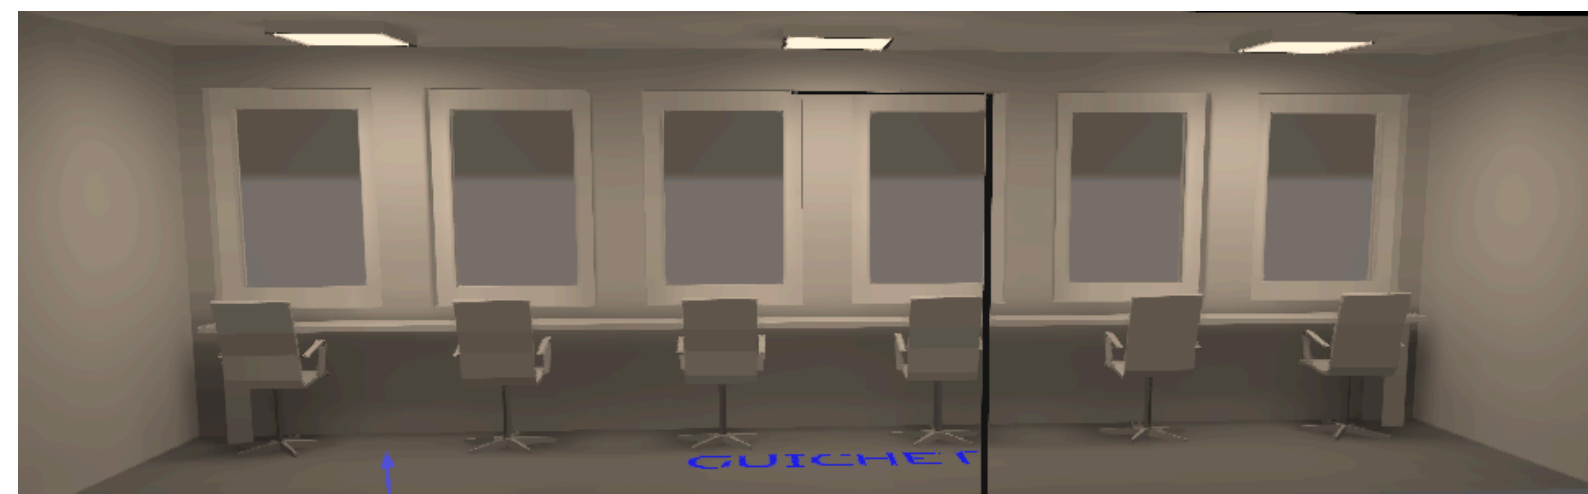


GUICHET

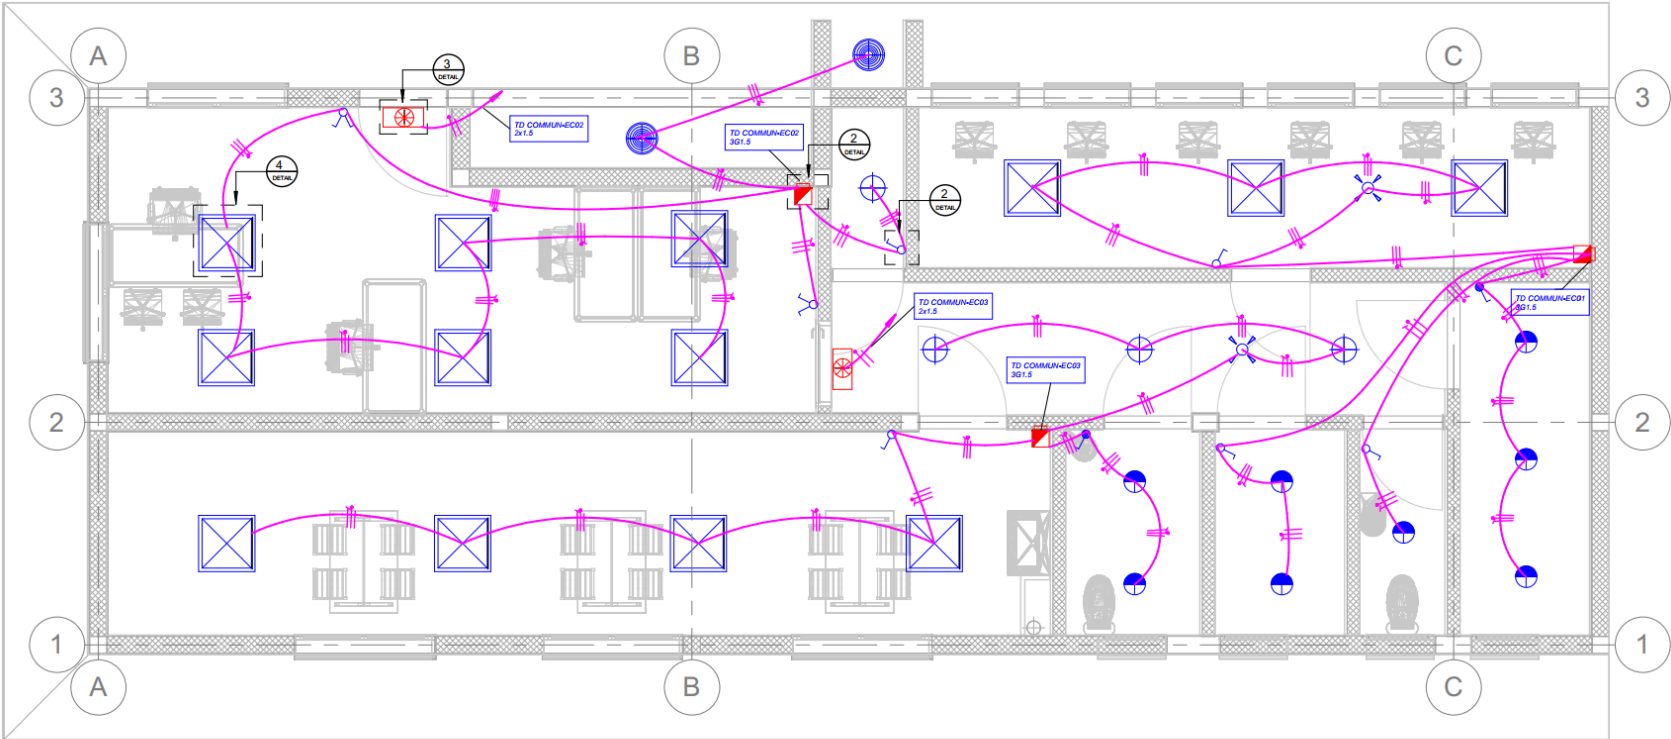


1 PLAN ECLAIRAGE ET ECLAIRAGE DE SECURITE_RDC
1 : 50

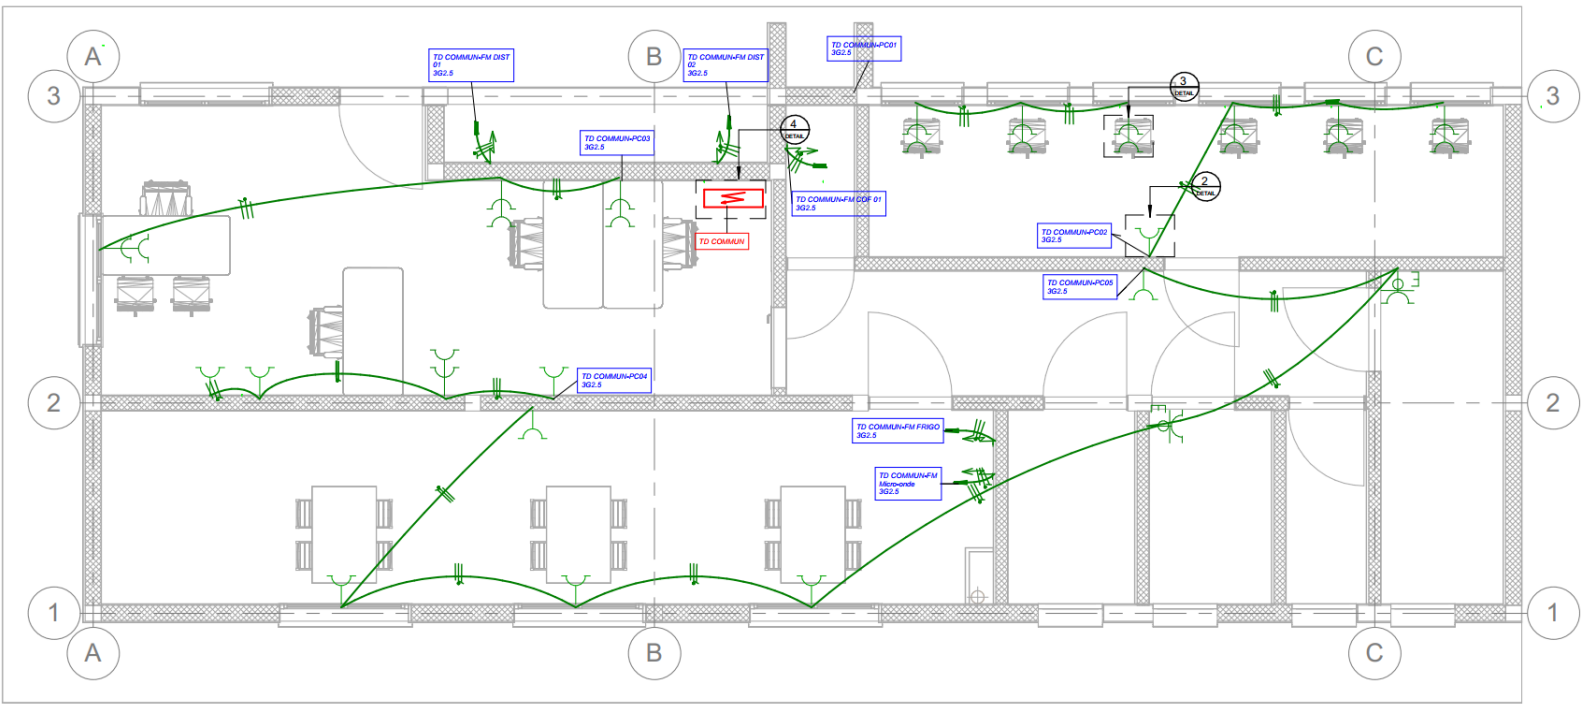

1 Plan prise courant et alimentation divers-RDC
1 : 50

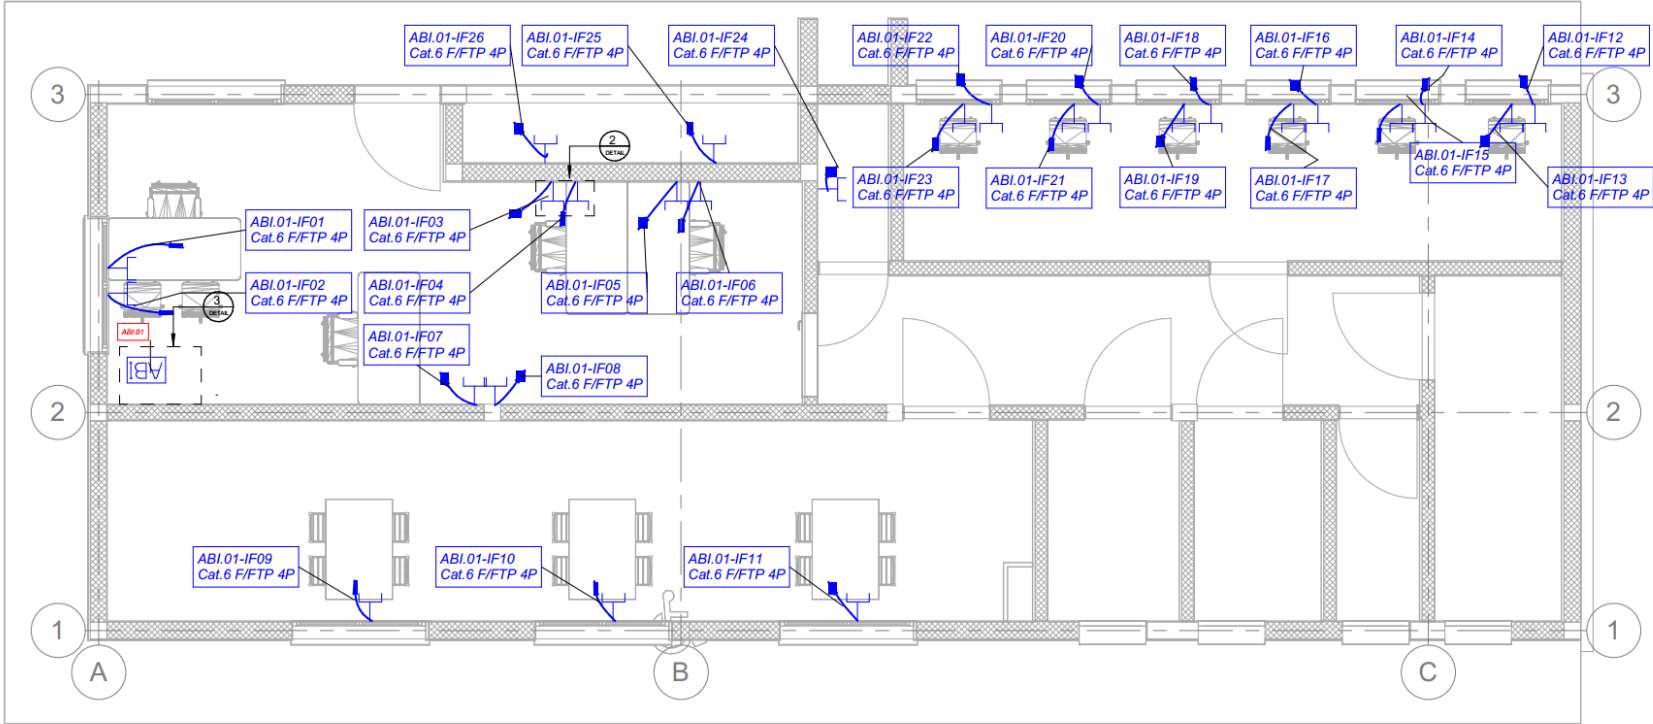


1 PLAN DE PRECABLAGE INFORMATIQUE-RDC
1 : 50

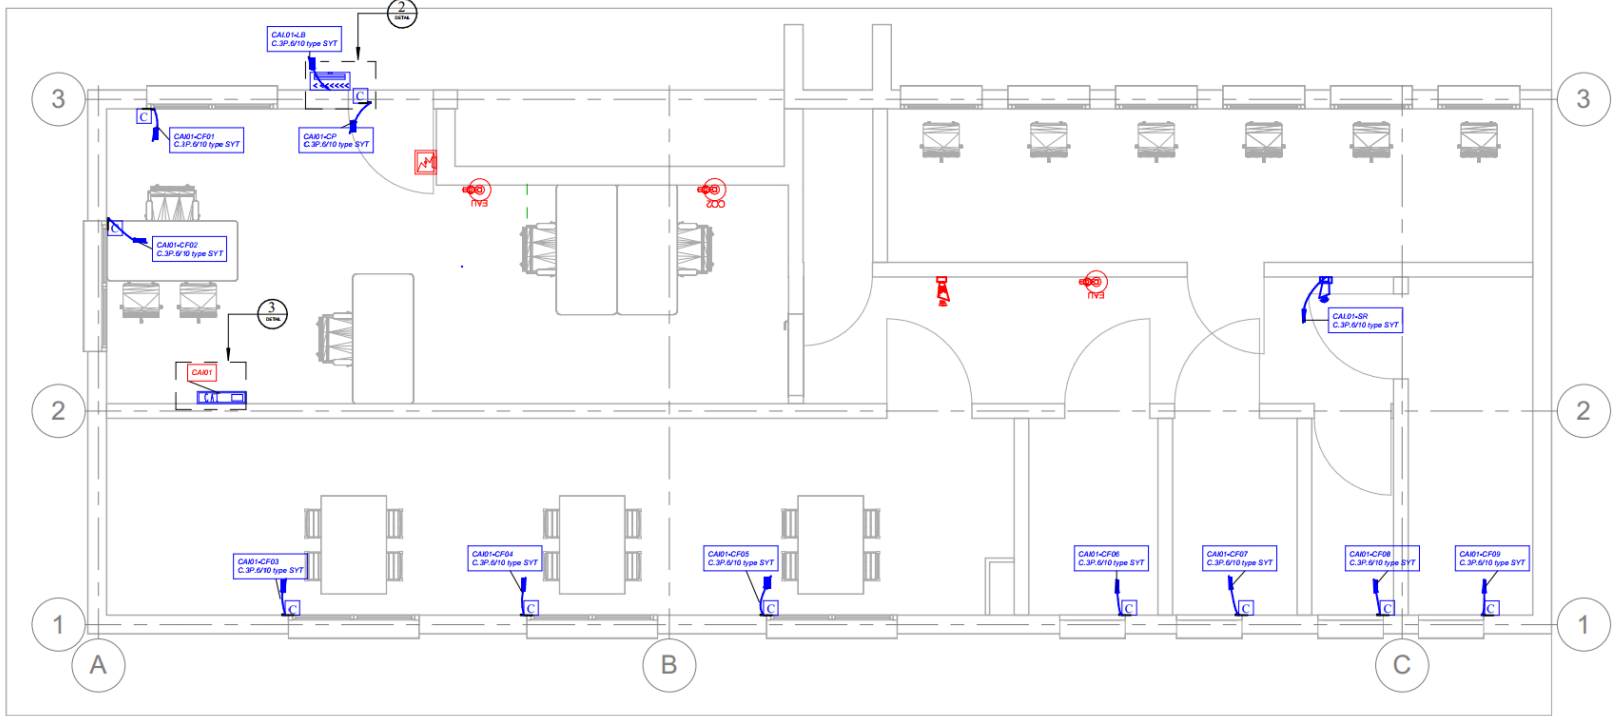


1 PLANE DE SYSTEME DE SECURITE_RDC Y COMPRIS LES EXTINCTEUR
1 : 50

PROJET 2

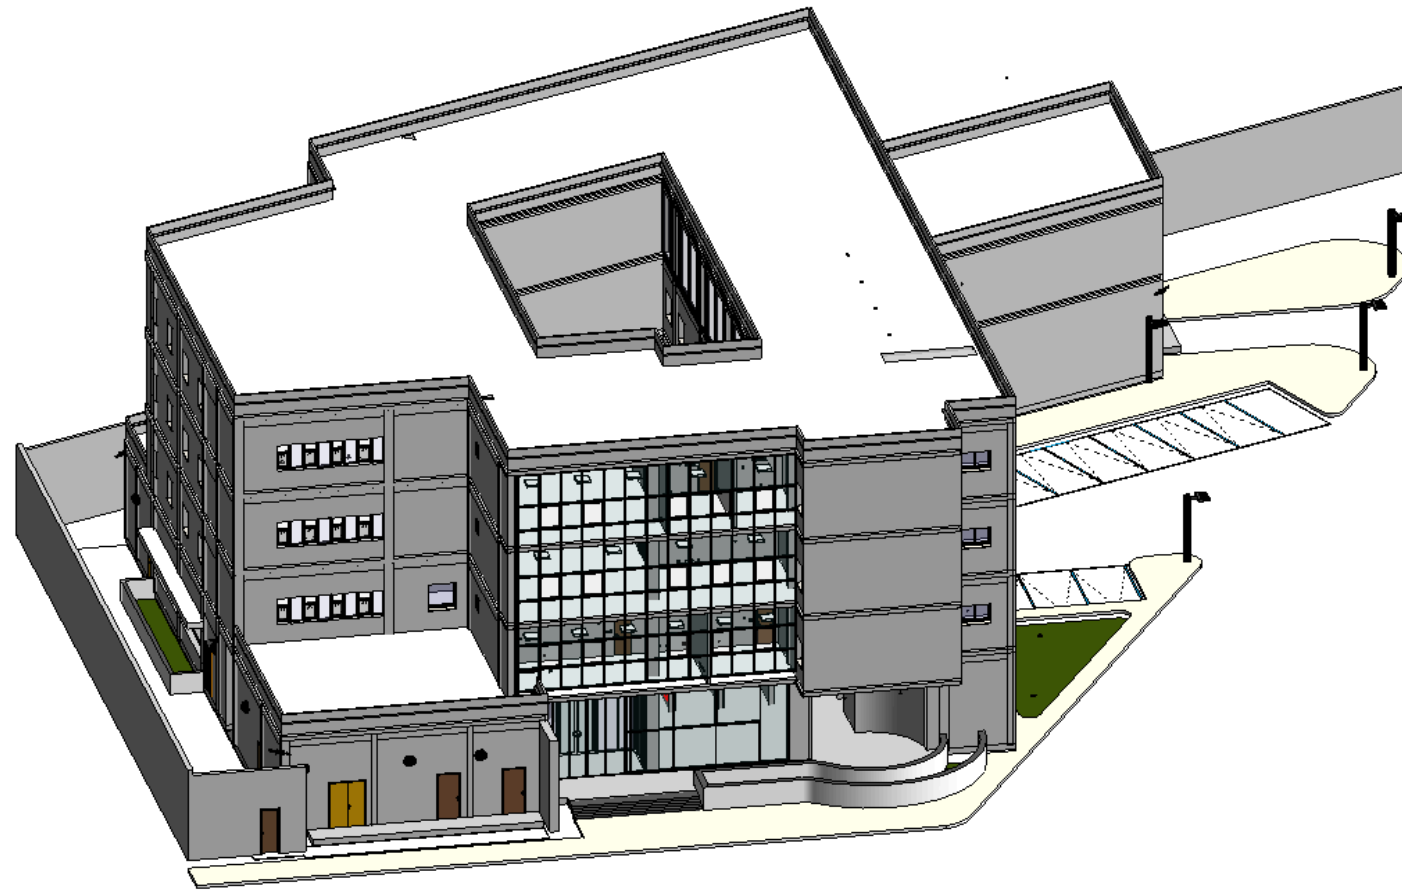


PROJECT 2


Projet bureautique: Etudes electricite du siege de la haute autorité de la presse et de l'audiovisuell. le présent descriptif a pour objet la définition des travaux et fournitures du lot :
ELECTRICITE - COURANTS FORTS ET
COURANTS FAIBLES

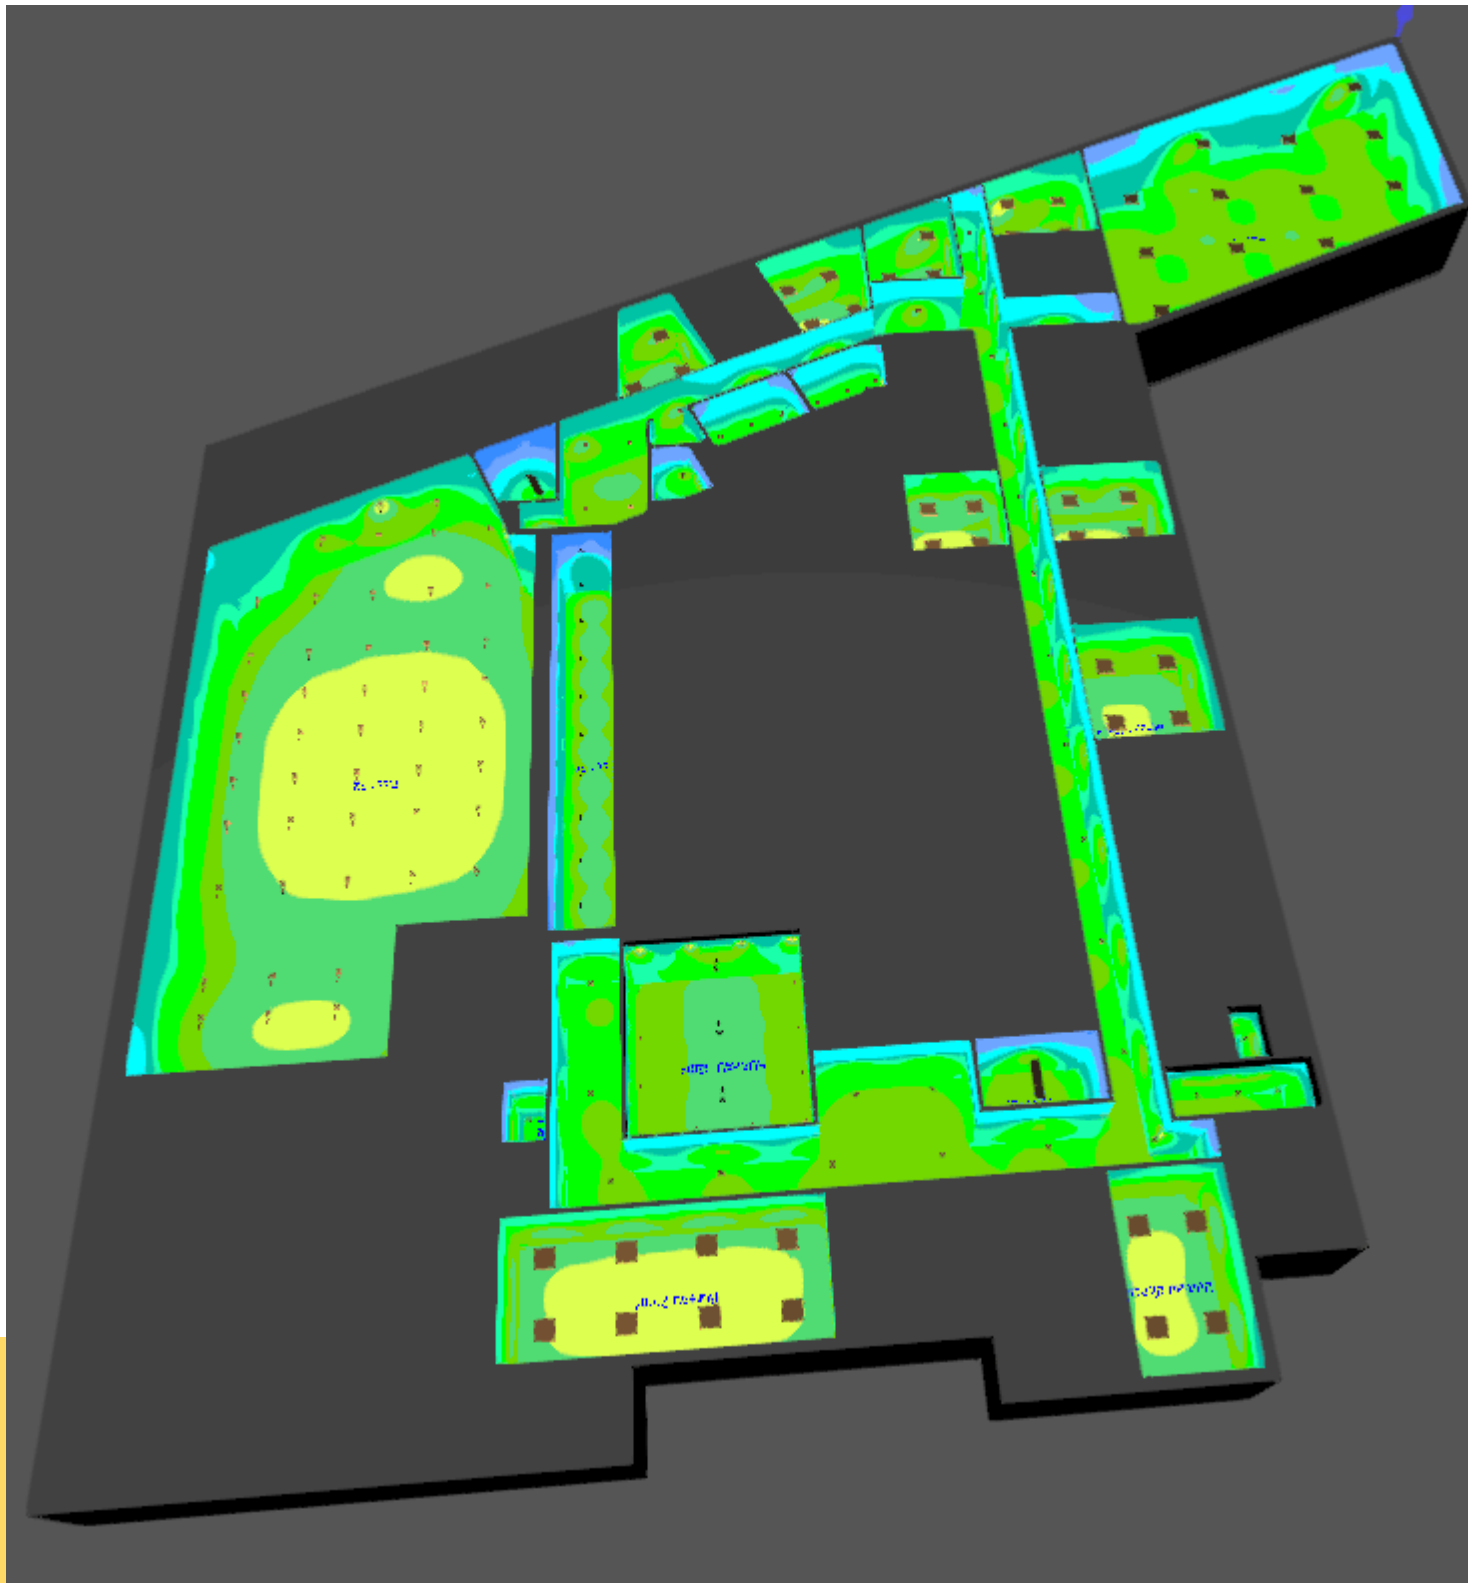


Plan RDC

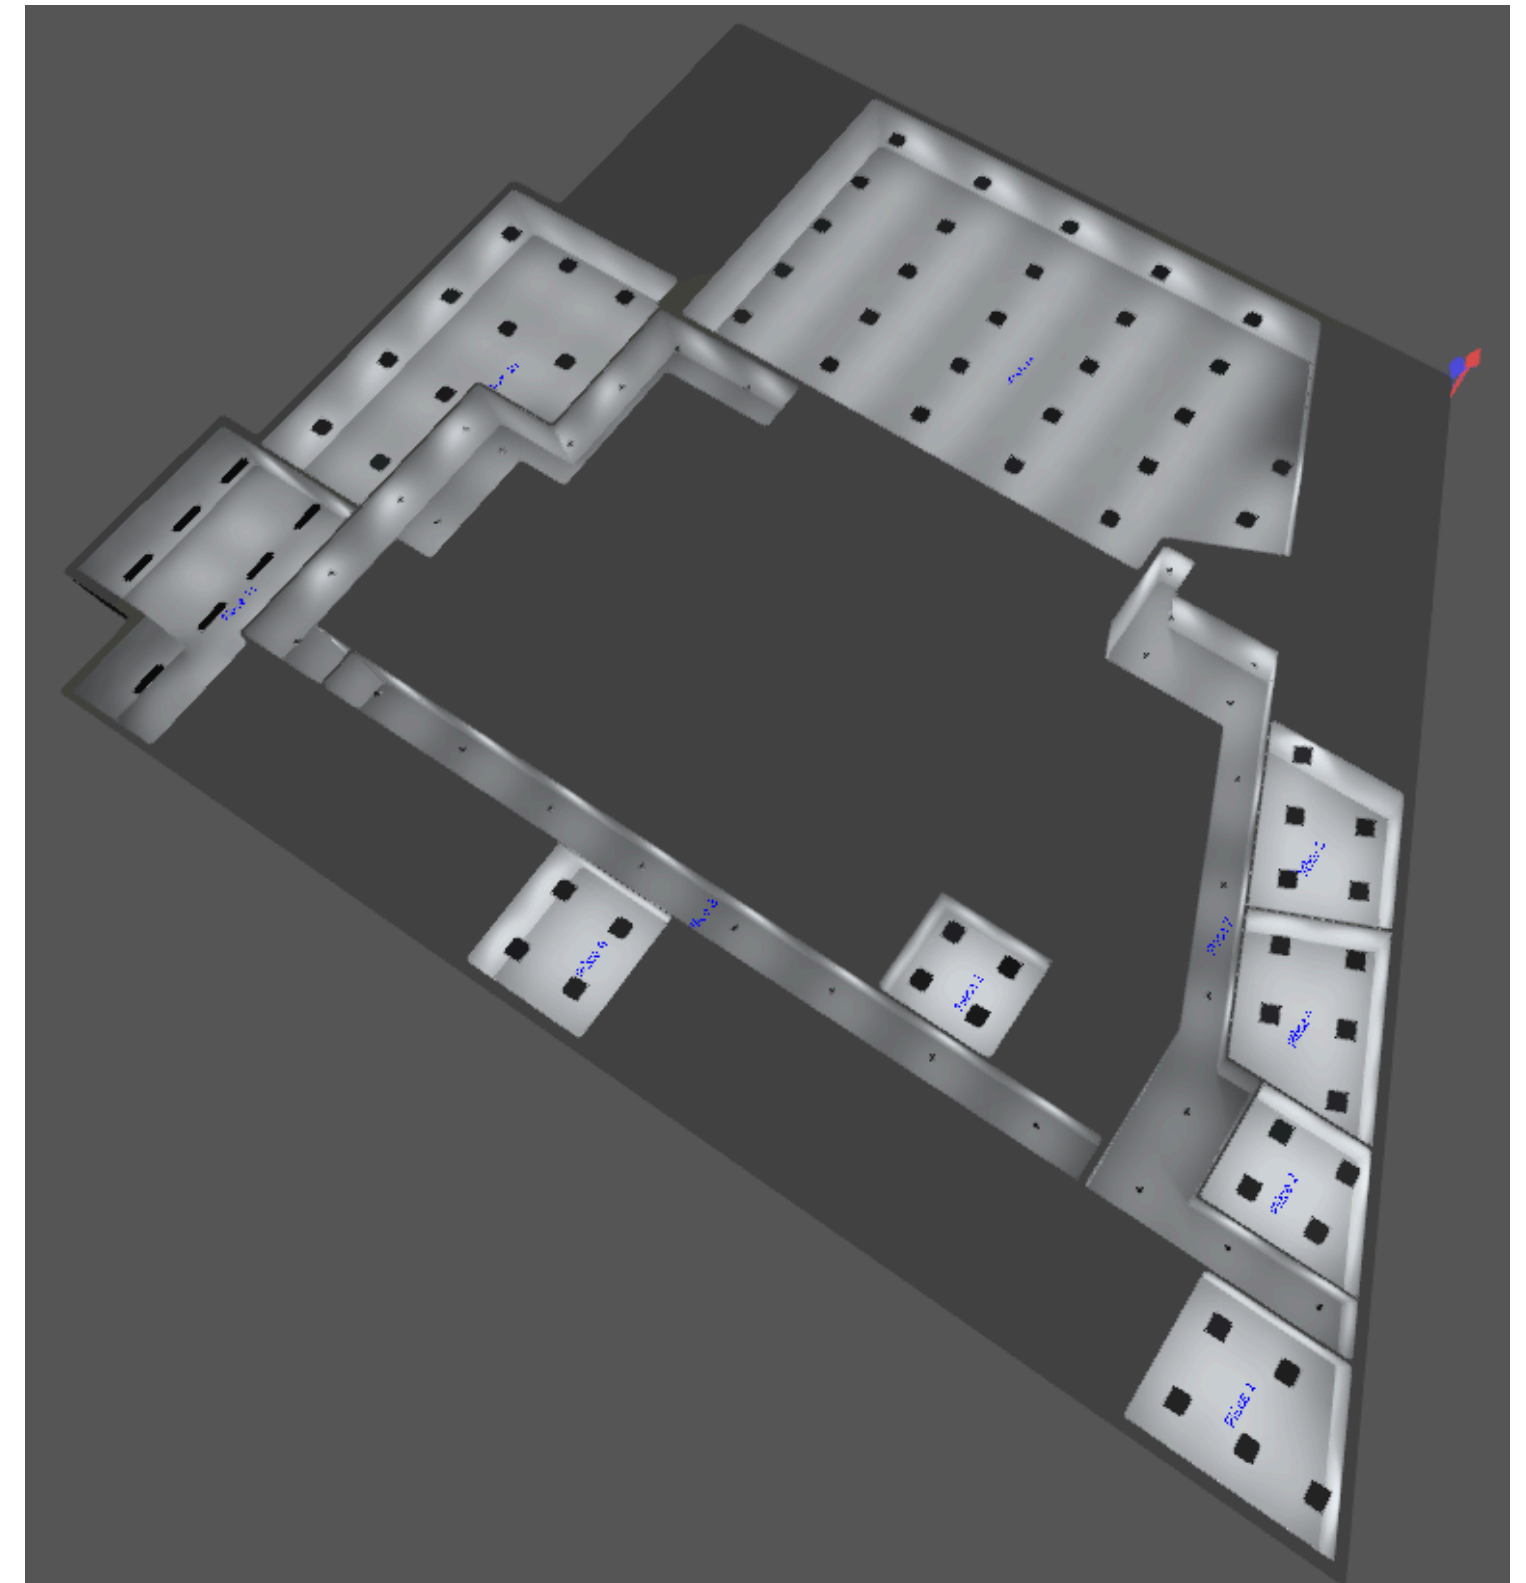



Plan ET1

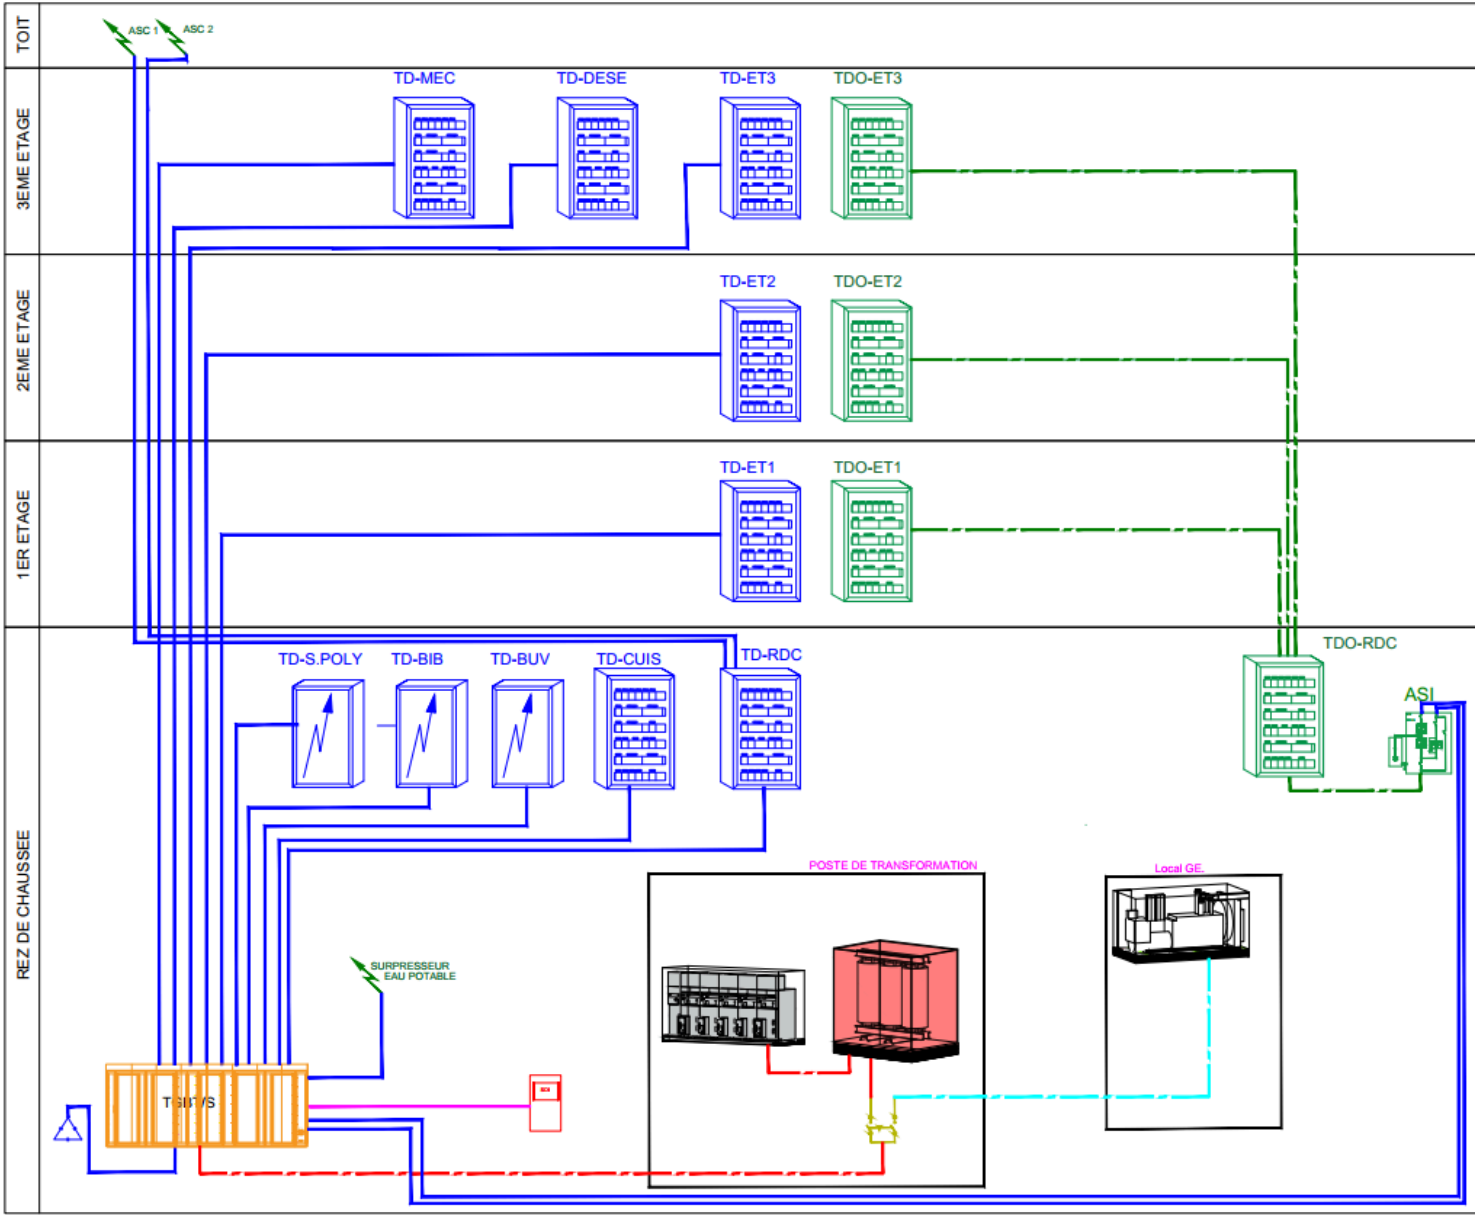

SYNOPTIQUE COURANT FORT

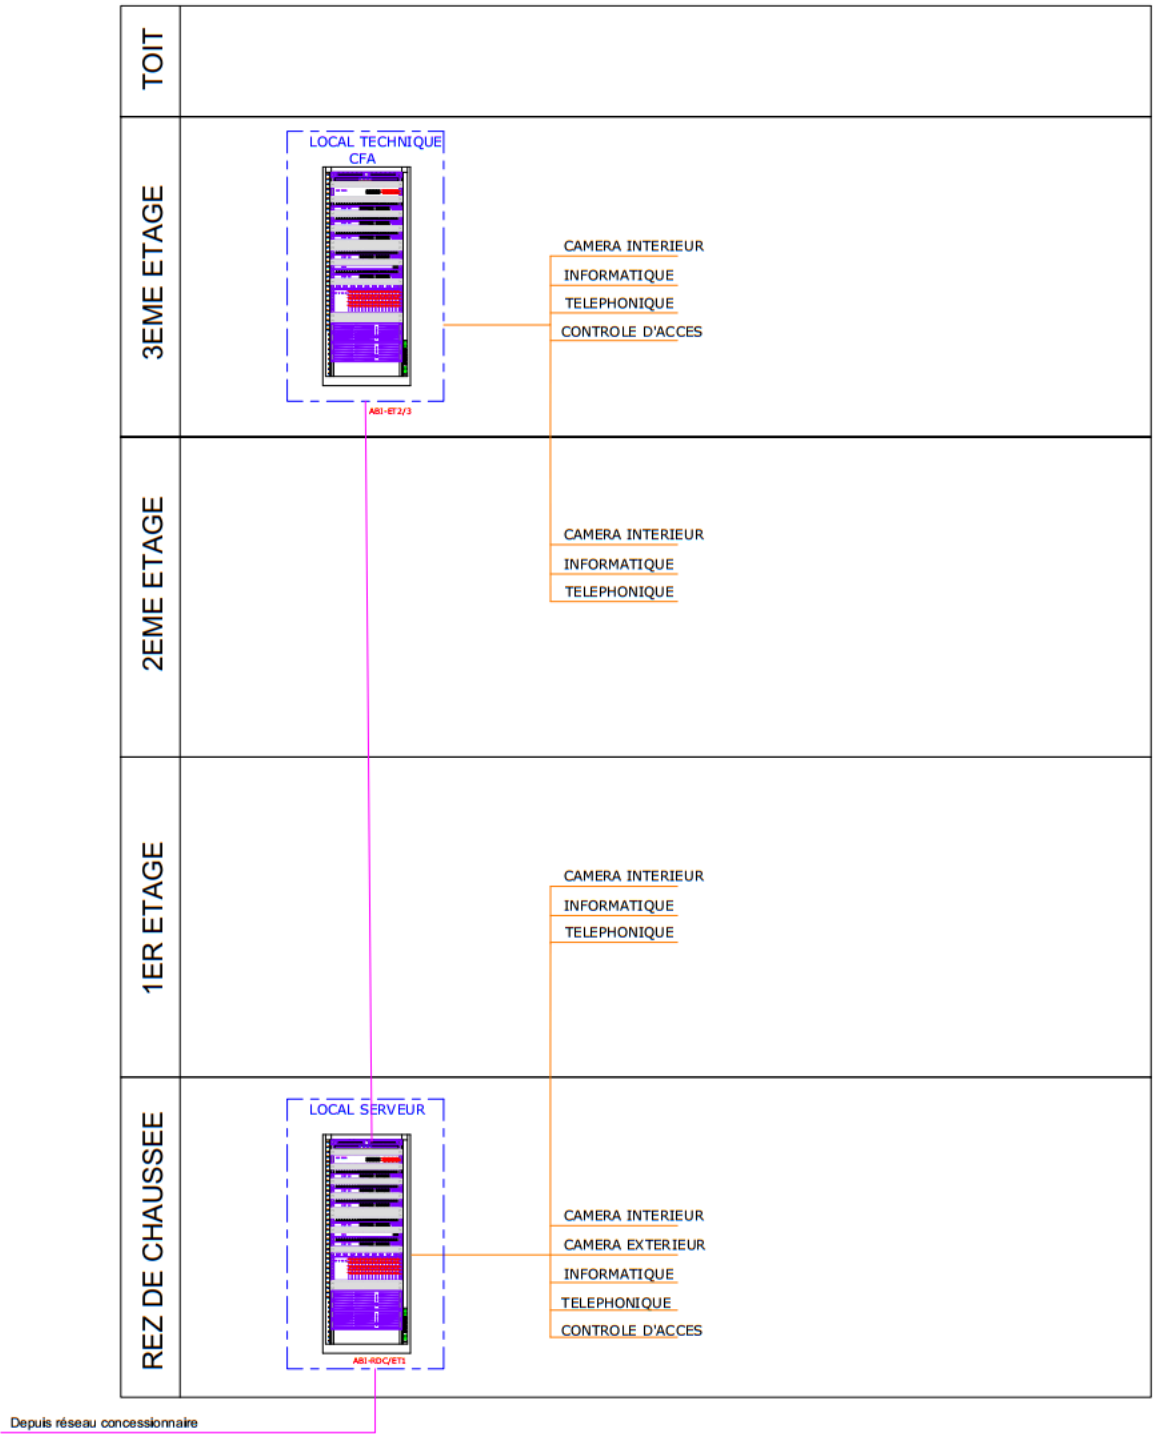


SYNOPTIQUE COURANT FAIBLE

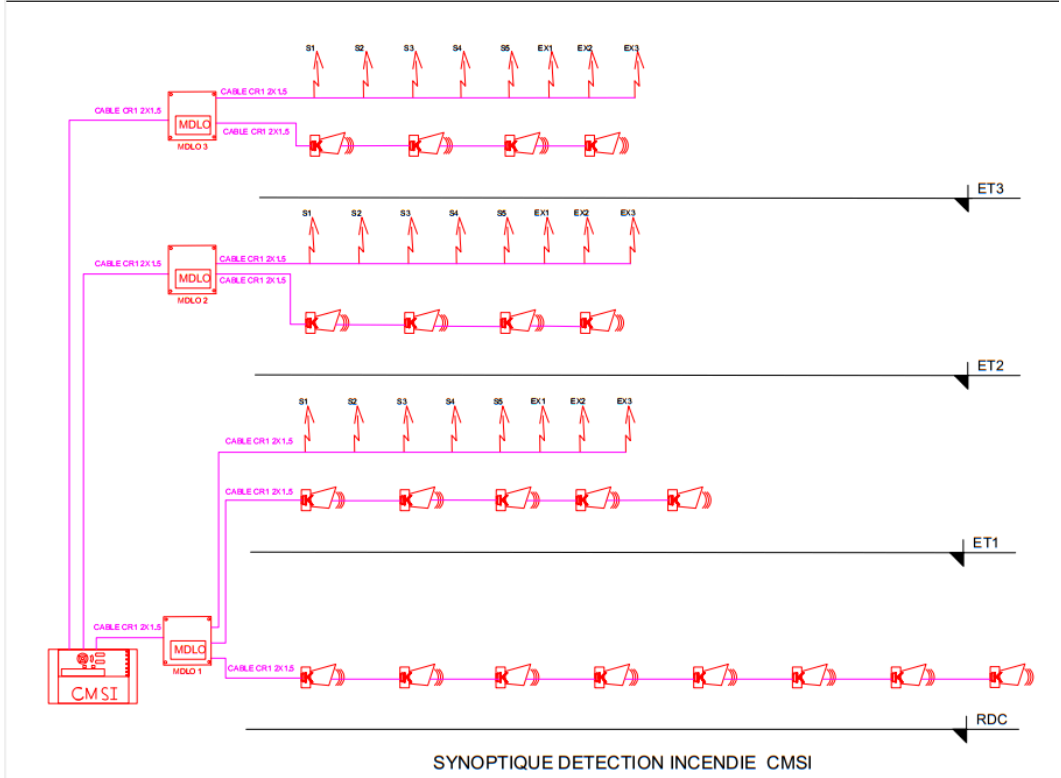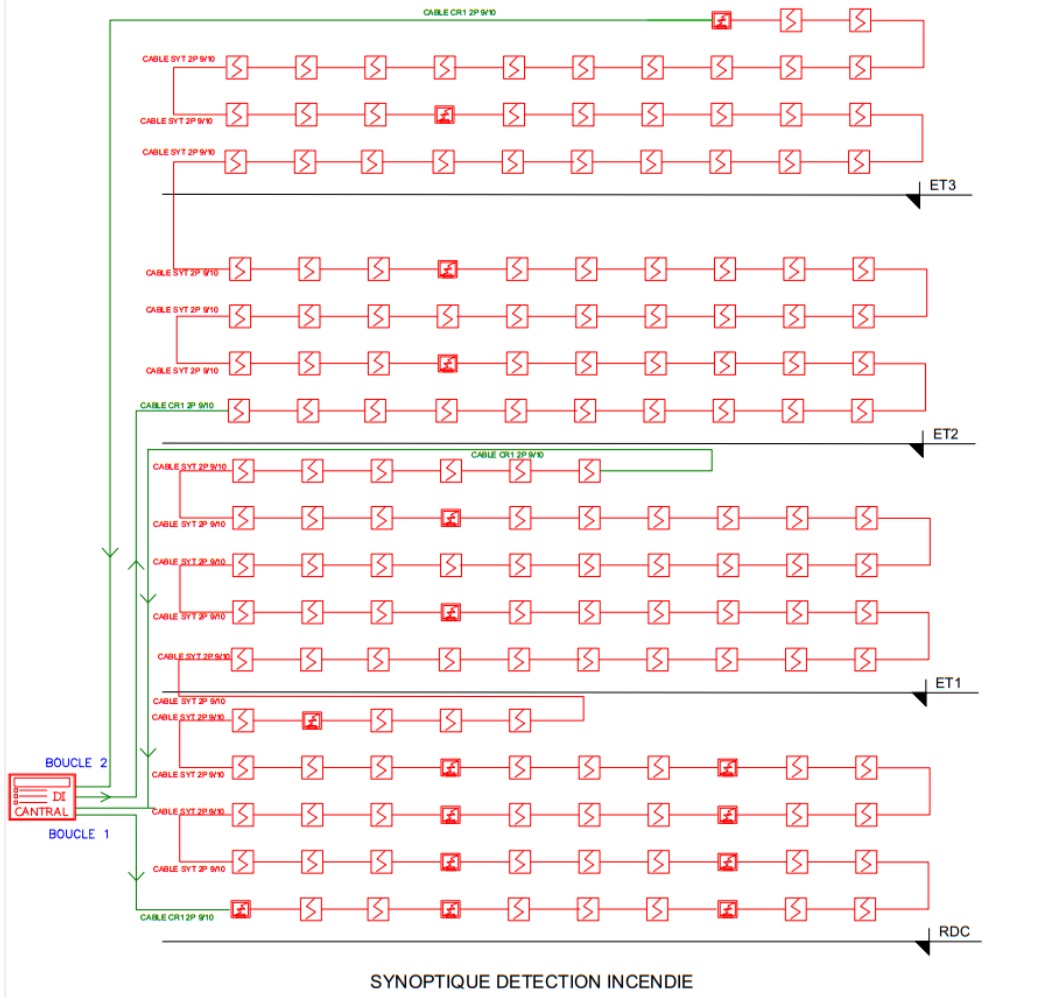


SYNOPTIQUE DETECTION INCENDIE



PLAN ECL RDC

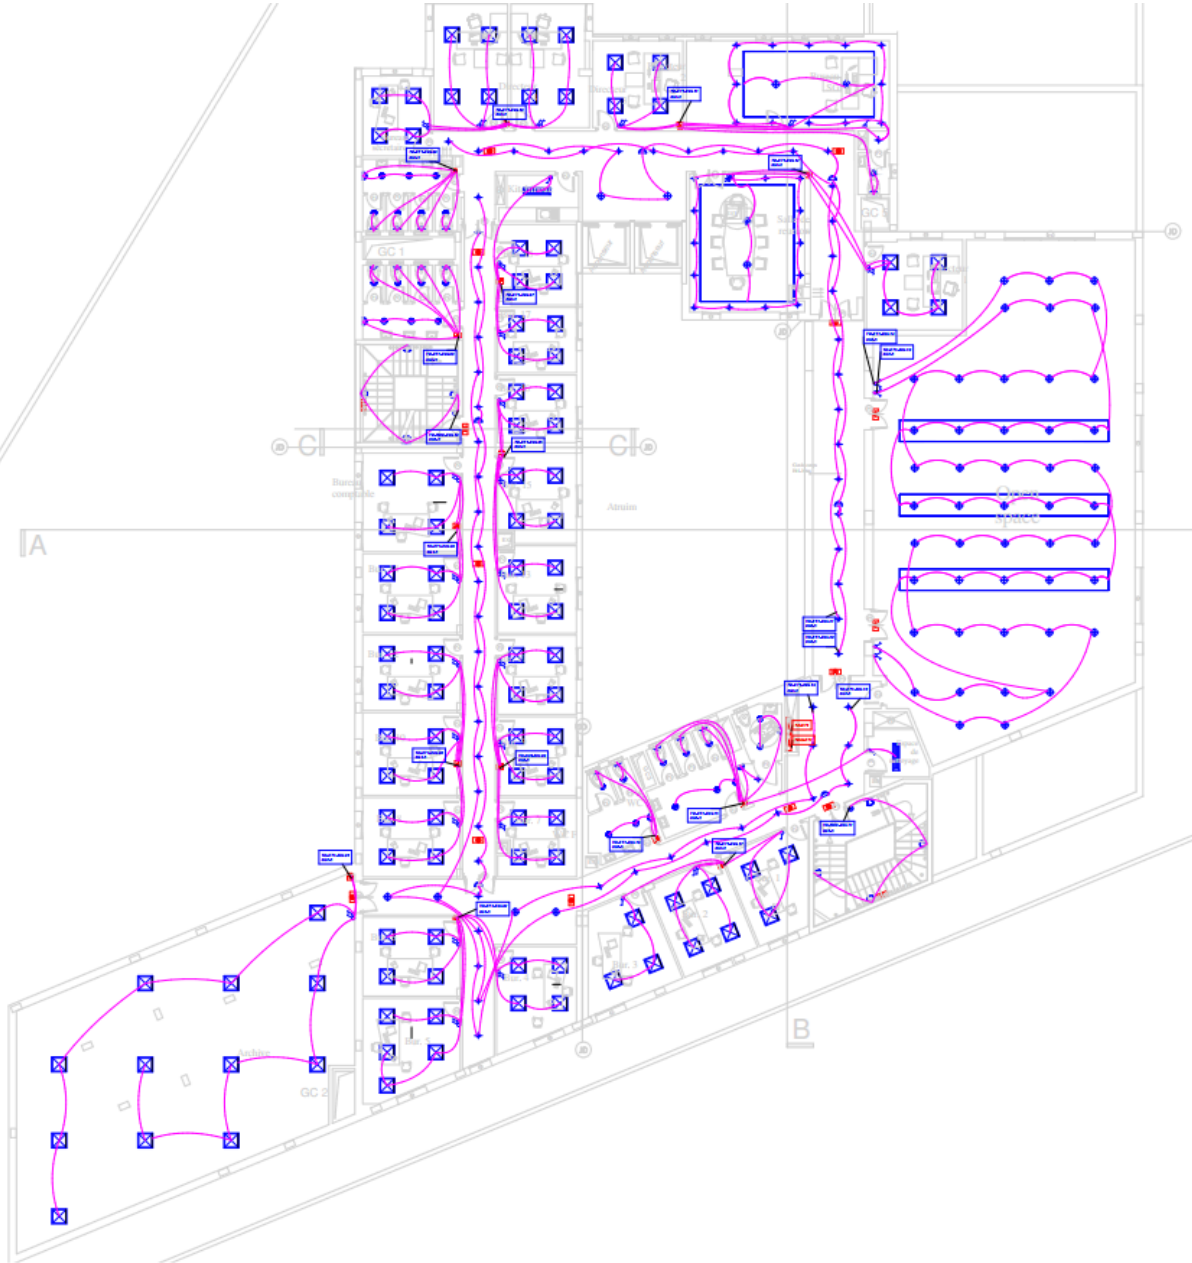




PLAN ECL ETAGE 1 ET ETAGE 2

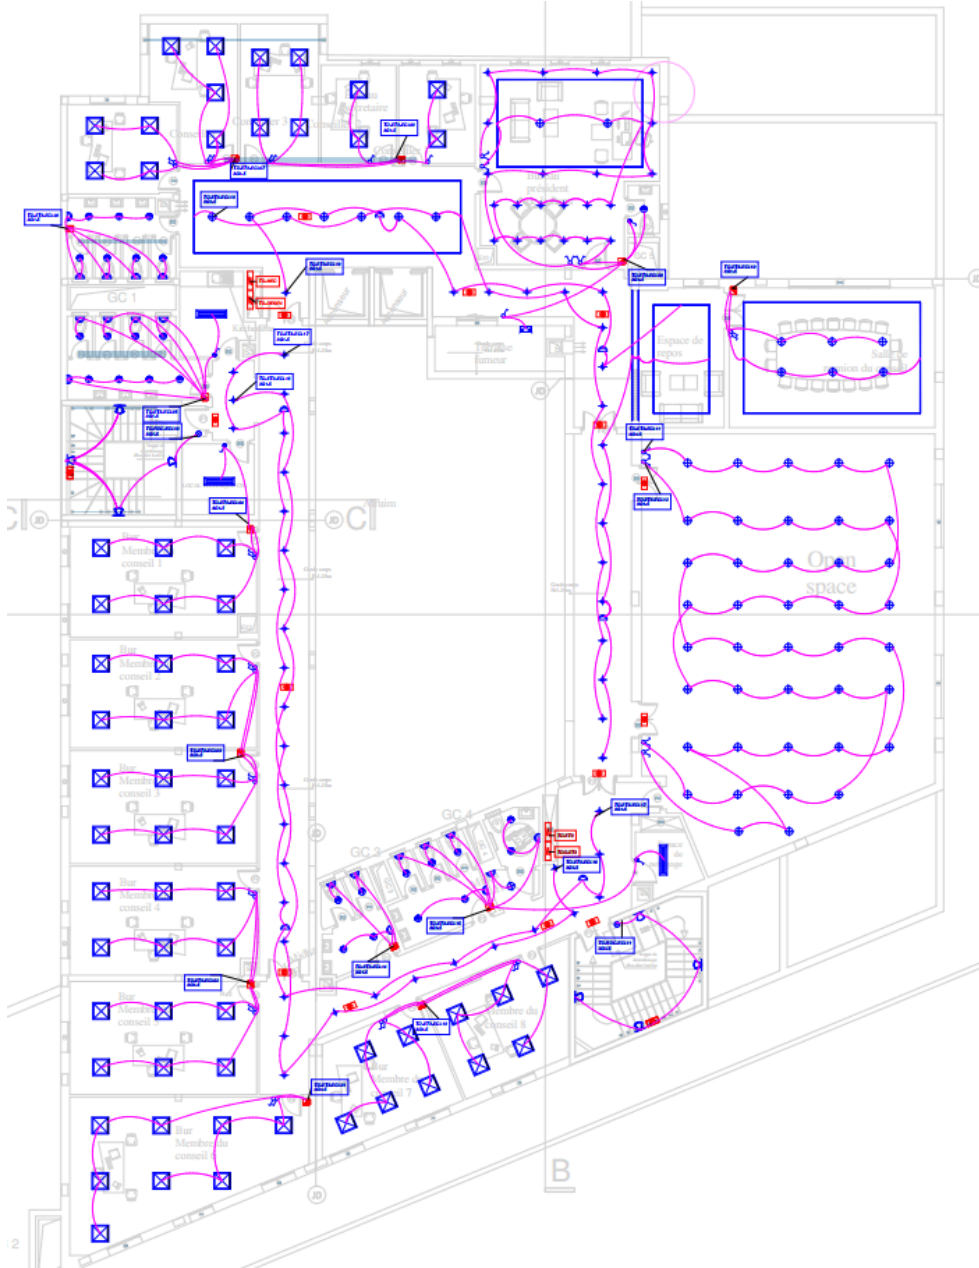

PLAN ECL ETAGE 3

LEGENDE ECLAIRAGE			
Symbole	Désignation	Symbole	Désignation
	Spot Led Encastre 22W		Applique Etanche IP65-25w
	Spot Led Encastre 6W		Detecteur de Mouvement
	Spot Led Encastre 10W		Interrupteur Simple Allumage
	Spot Led Encastre 32W		Interrupteur Va et Vient
	Dalle Corne Led 36w		Interrupteur Simple Allumage Etanche
	Diffuseur a Grille 1200mm-22w		Interrupteur Va et Vient Etanche
	Luminaire Led Etanche IP65 1200mm-22w		Bloc Autonomes 60 Lumens
	Spot a Encastrer au Sol IP66-12w		Tableau de Commande
	Ruban Led 10w/m		Boite de Derivation
	Applique Led Decoratifs 25w		Coffret Electrique Encastre
	Lampadaire Urbain Led IP66-25w		

LEGEND ECL

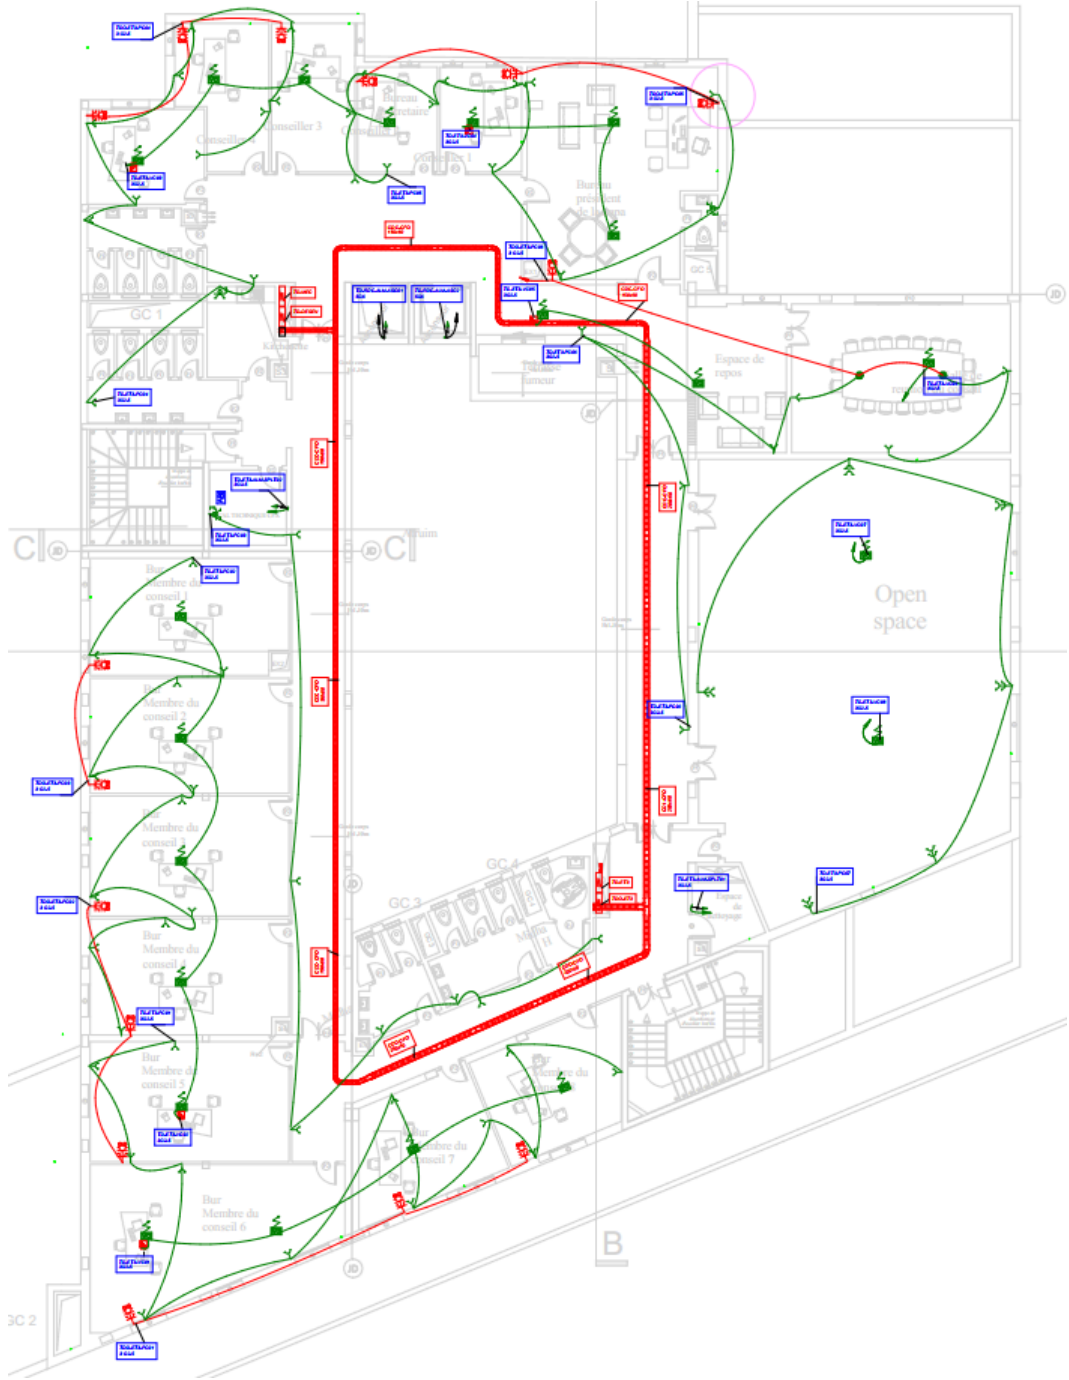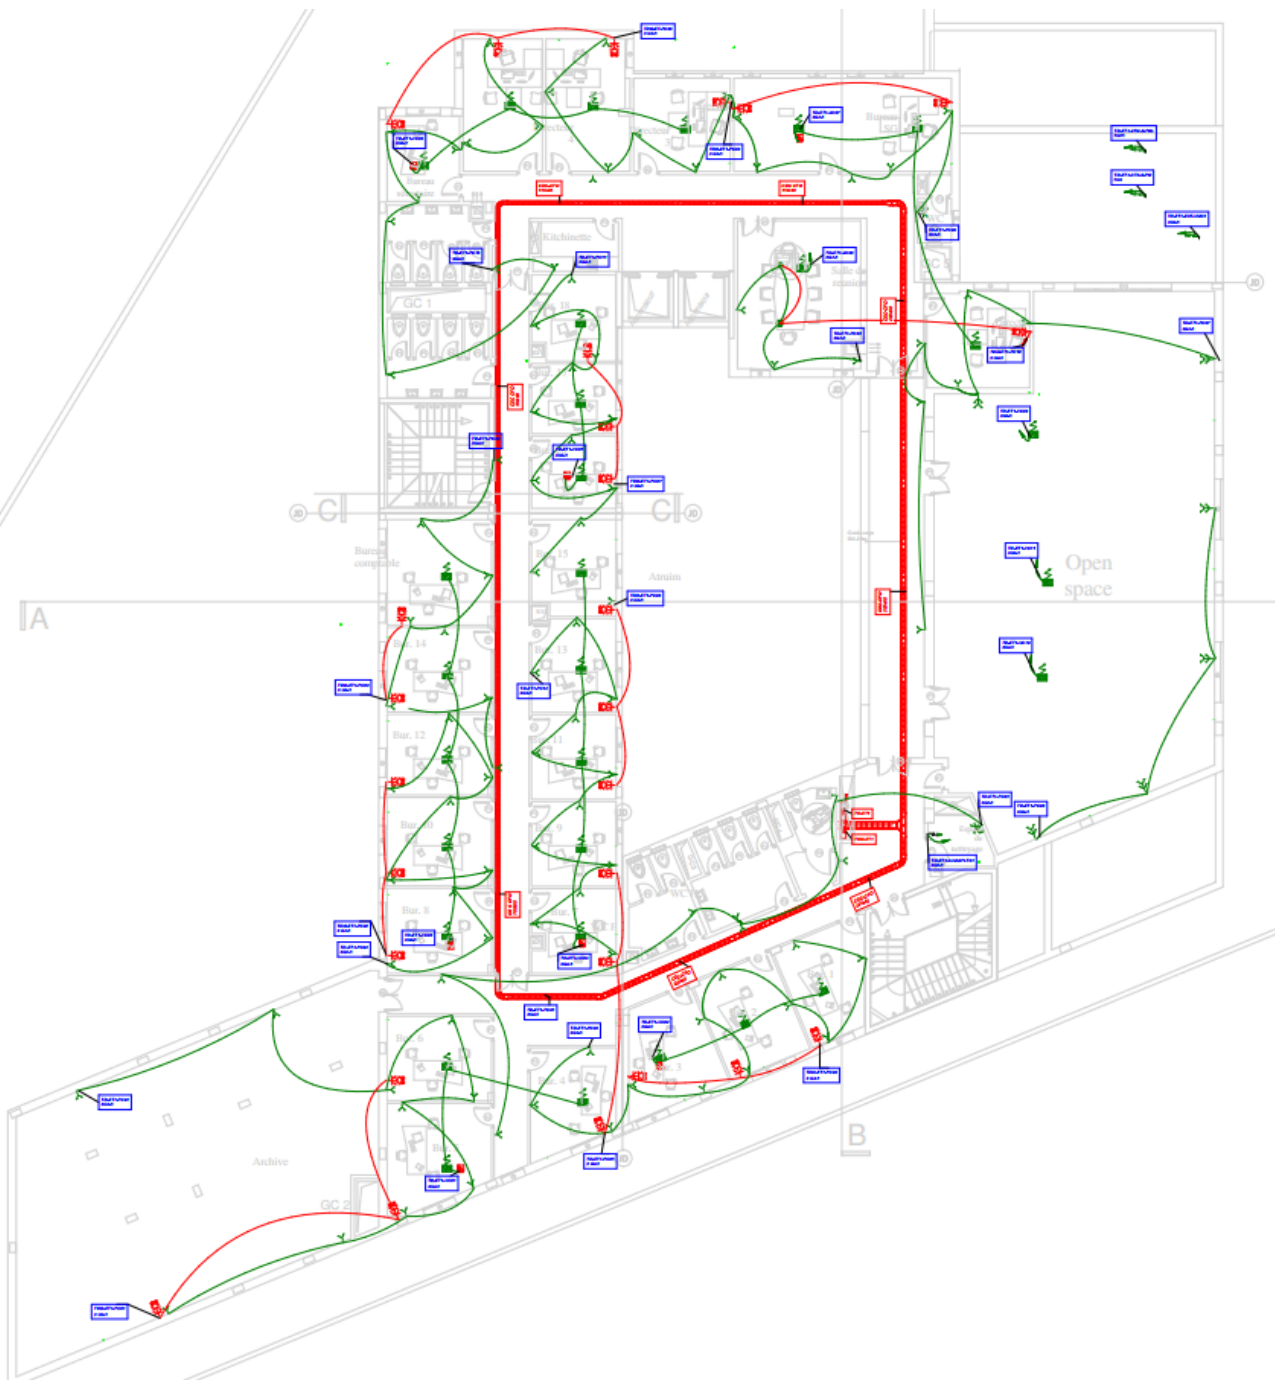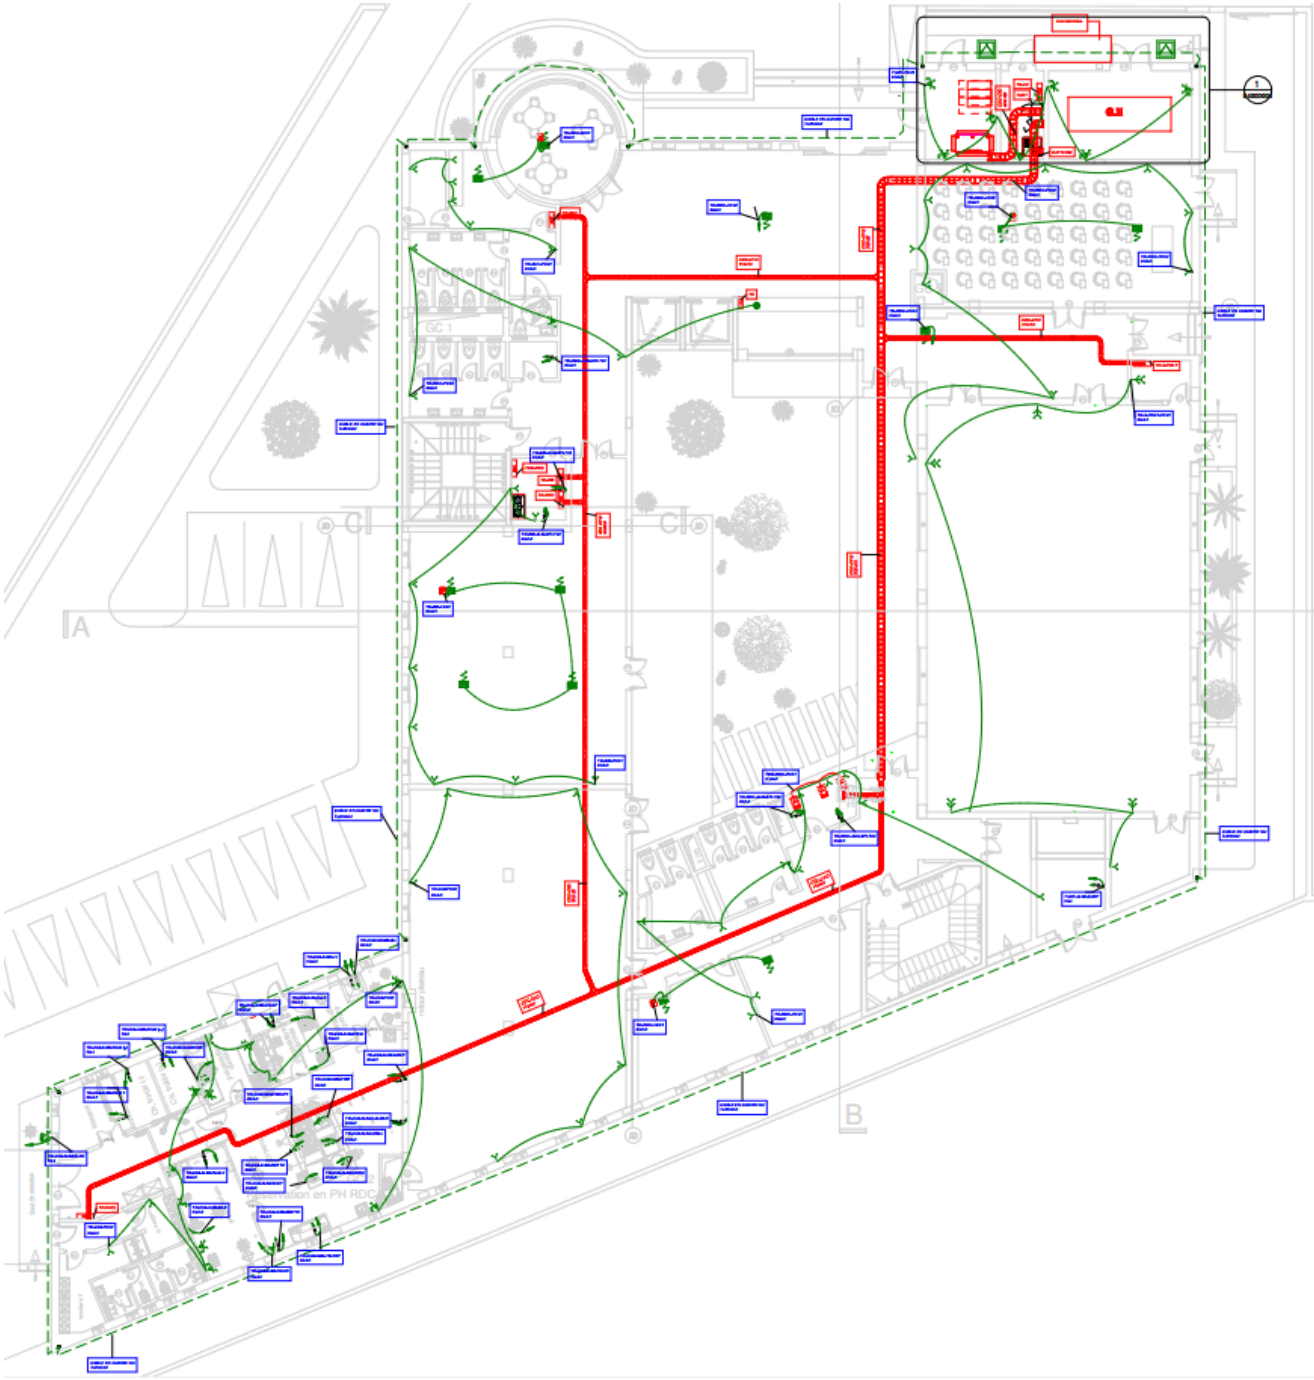

PLAN CFO RDC



PLAN CFO ETAGE 1 ET ETAGE 2

PLAN CFO ETAGE 3

LEGENDE PRISE COURANT -PCA-			
Symbole	Désignation	Symbole	Désignation
	Prise de Courant 2P+T 10/16A		Fond de Fouille en Cuivre Nu de 35mm2
	Prise de Courant Etanche 2P+T 10/16A		Liaison Equipotentiel
	Prise de Courant Ondule		Armoire Electrique
	Boite au Sol Comprenant 4 Prises de Courant 2P+T 10/16A		Alimentation Vento Convector
	Boite de Derivation PC		Alimentation en Attente VMC
	Regard de Terre de 80x80x80		

LEGENDE CHEMINS DE CABLE	
Symbole	Désignation
	Chemins de Cable CFO
	Double Chemins de Cable CFO
	Raccord Chemins de Cable CFO

LEGEND CFO

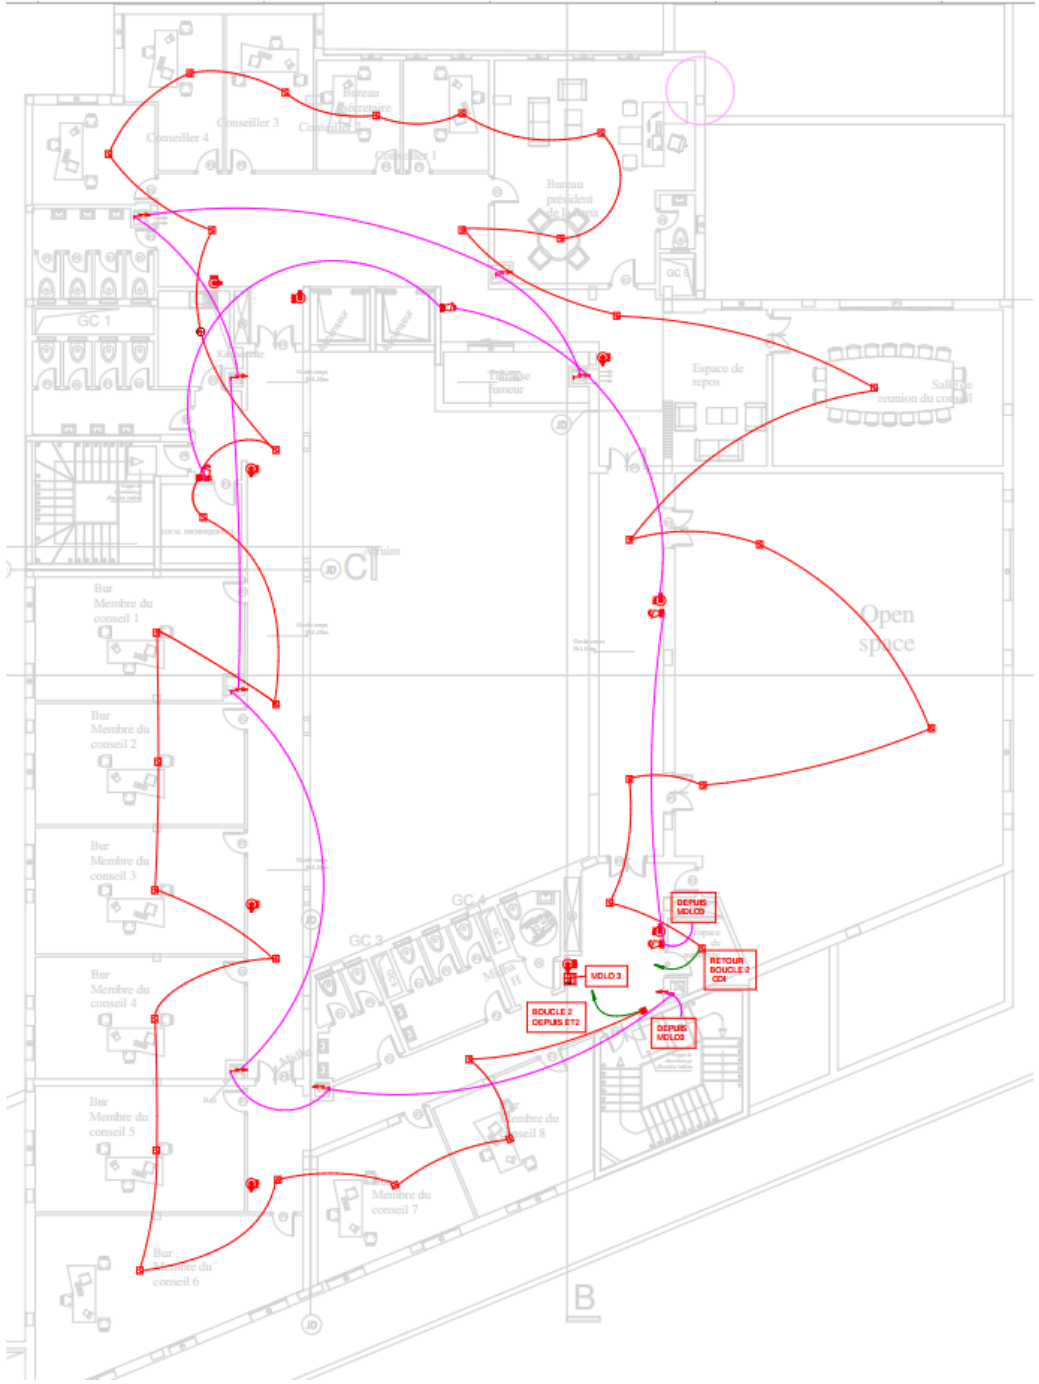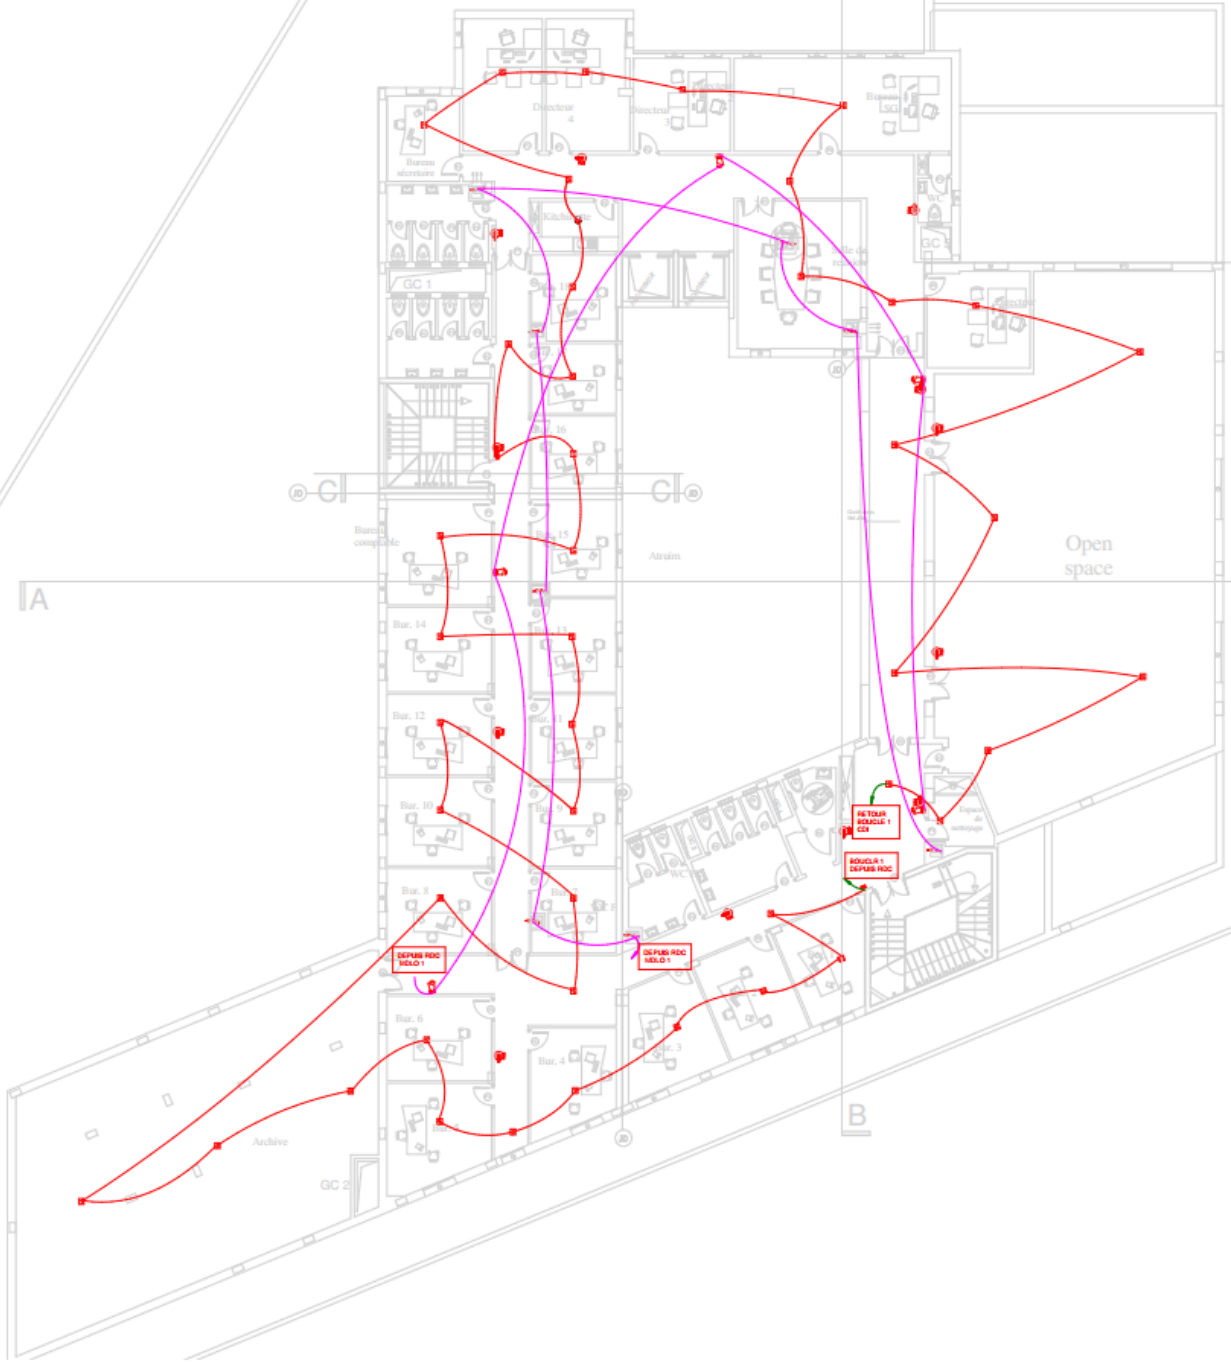





PLAN SDI RDC

PLAN SDI ETAGE 1 ET ETAGE 2


PLAN SDI ETAGE 3

LEGENDE SECURITE INCENDIE -SSI-			
Symbole	Désignation	Symbole	Désignation
	Dectecteur Thermique de Fumee		Centrale de Detection Incendie
	Dectecteur de Fuite de Gaz		Centrale de Mise Securite Incendie
	Dectecteur Optique de Fumee		Extincteur Type CO2 5kg
	Boite a Brise de Glace		Extincteur a Eau Additif
	Klaxon d'Alarme		Alimentation en Attente DAS
	Cable CR1 2P 9/10		Cable CR1 2X1.5
	Cable SYT 2P 9/10		MODULE DEPORTEE ASSERVISSEMENT

LEGEND CFA

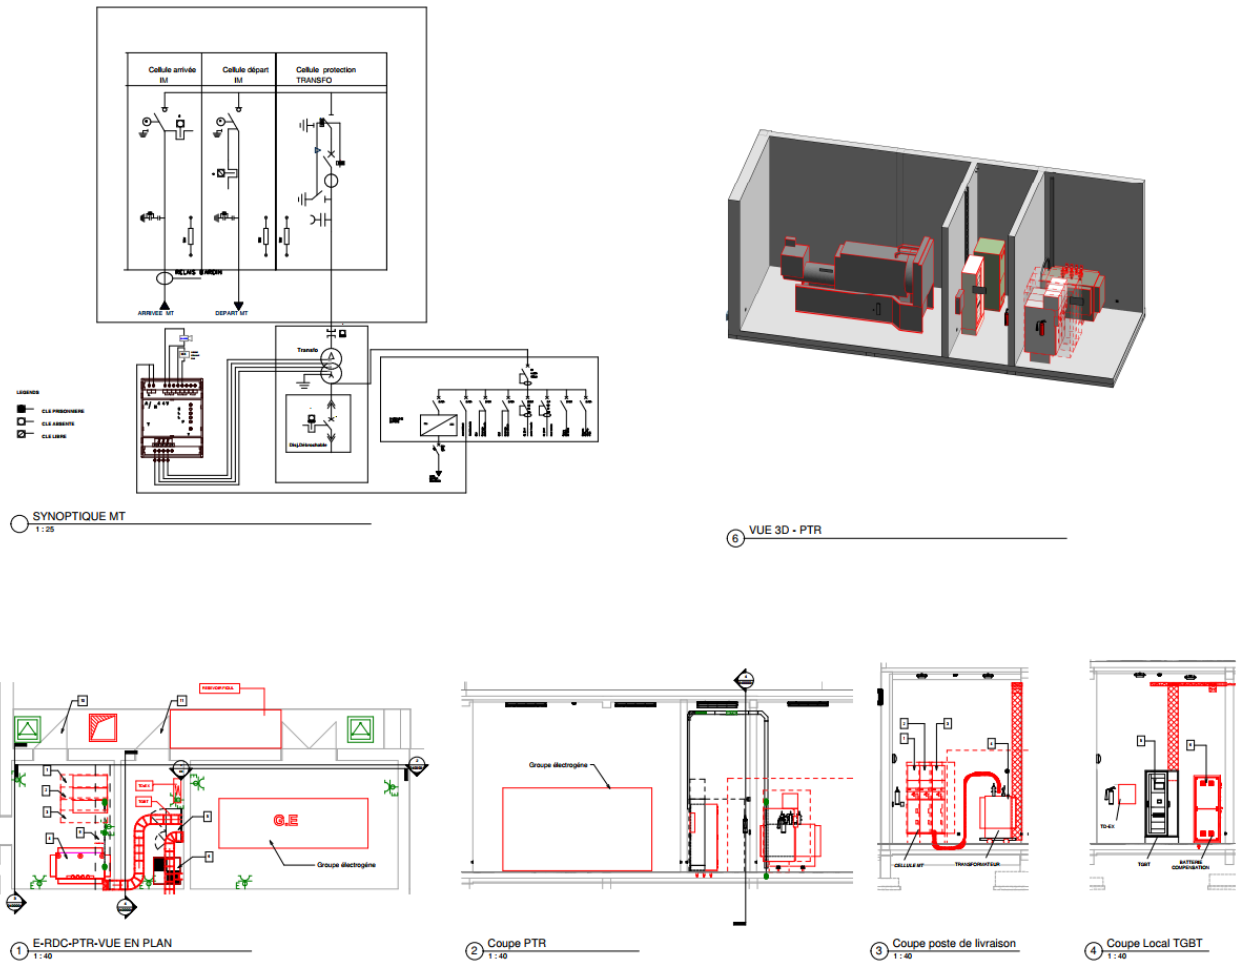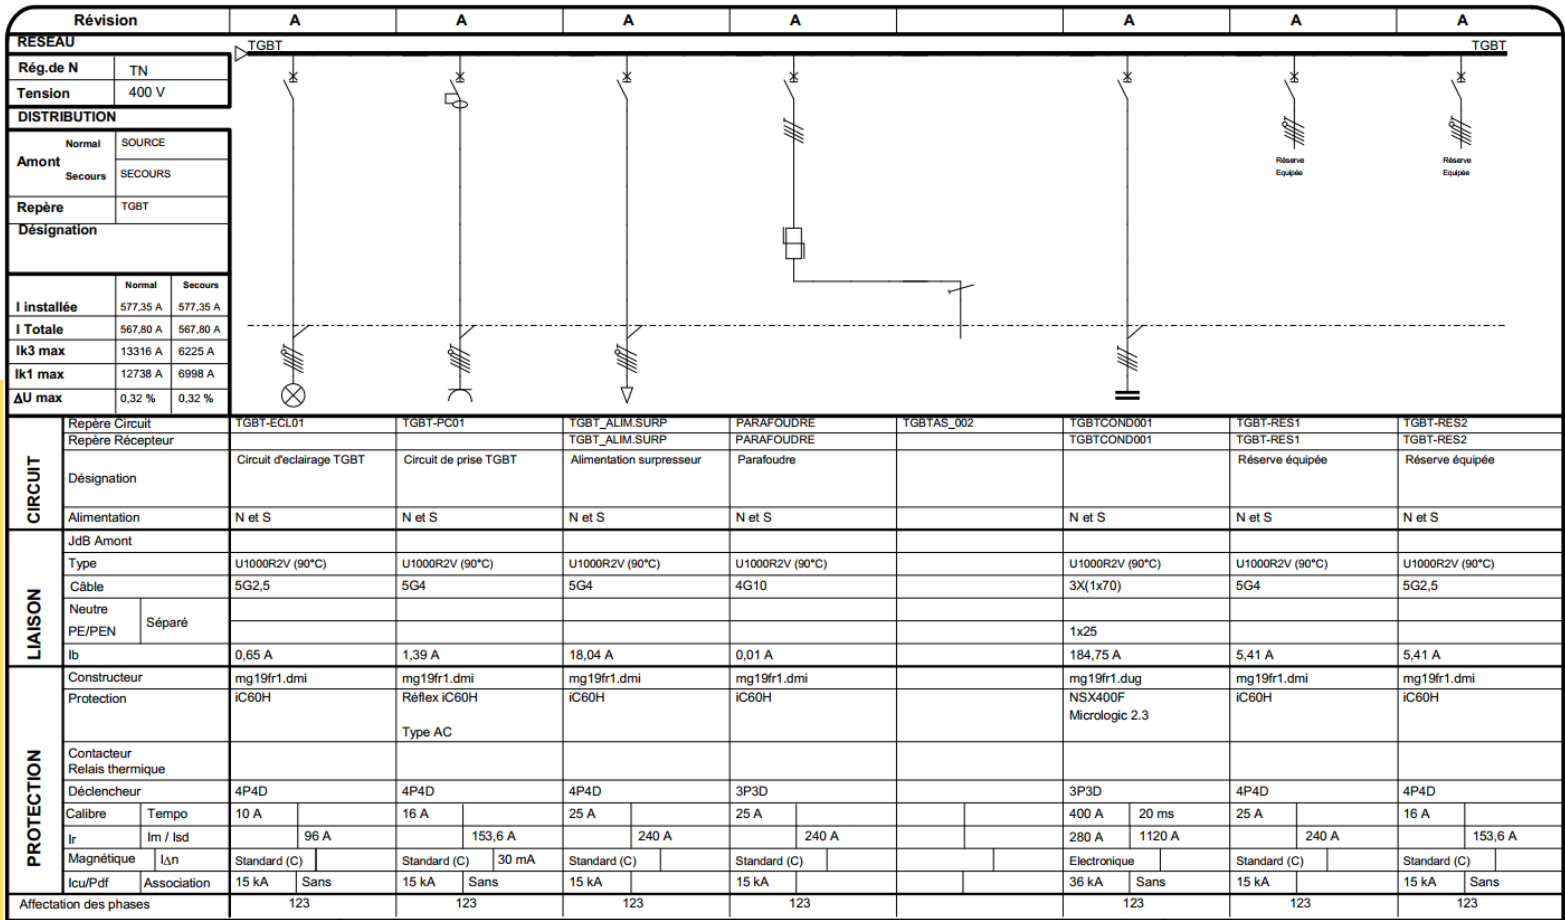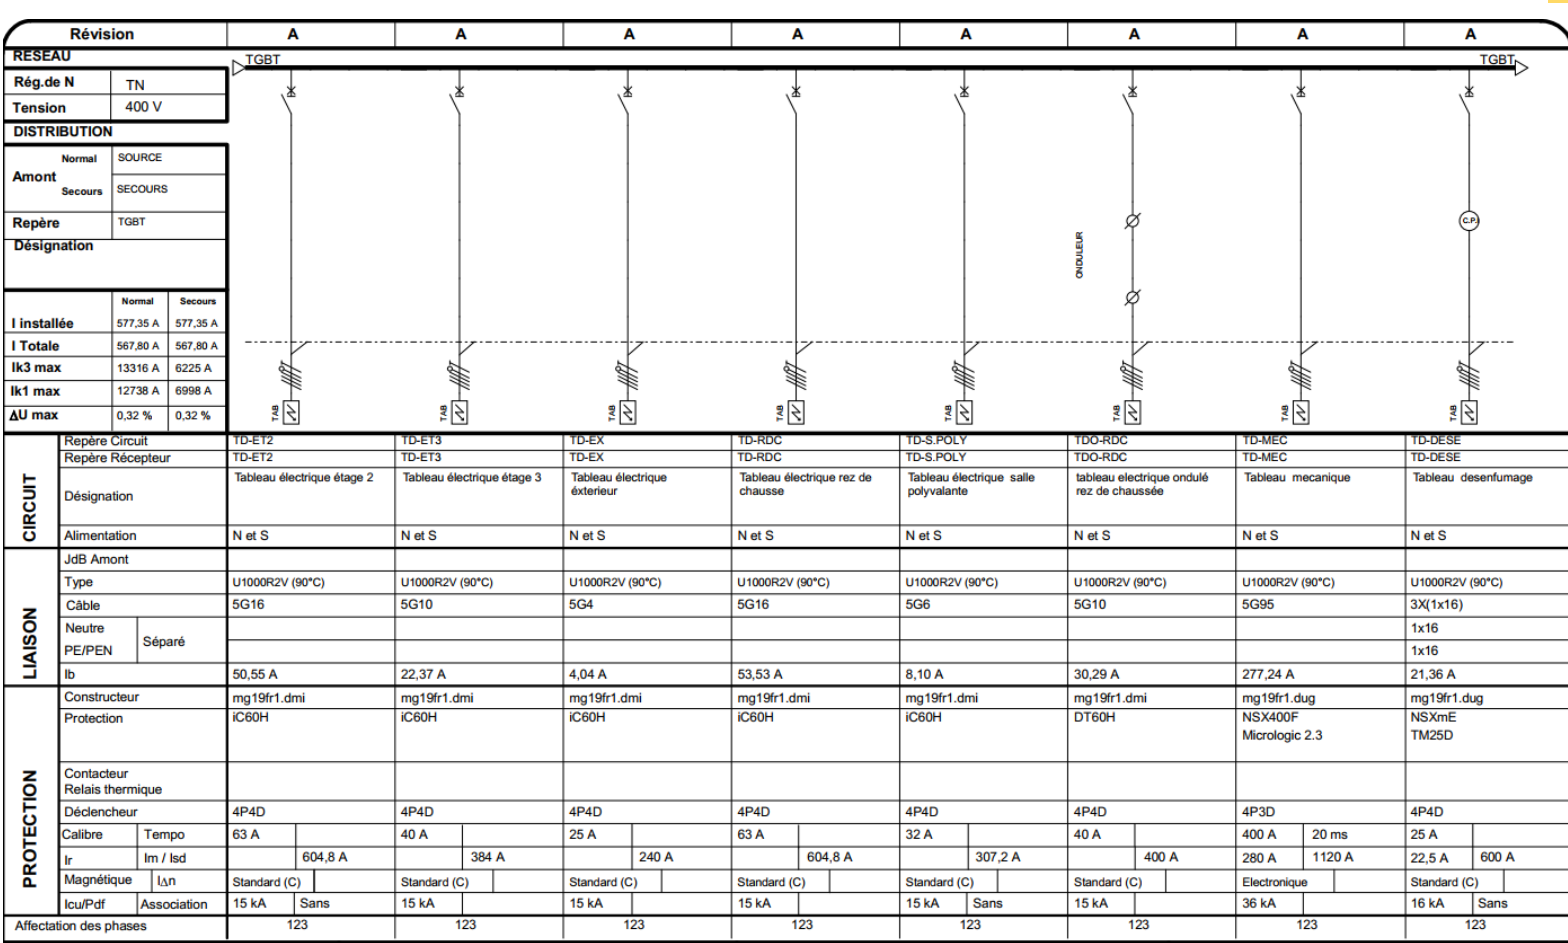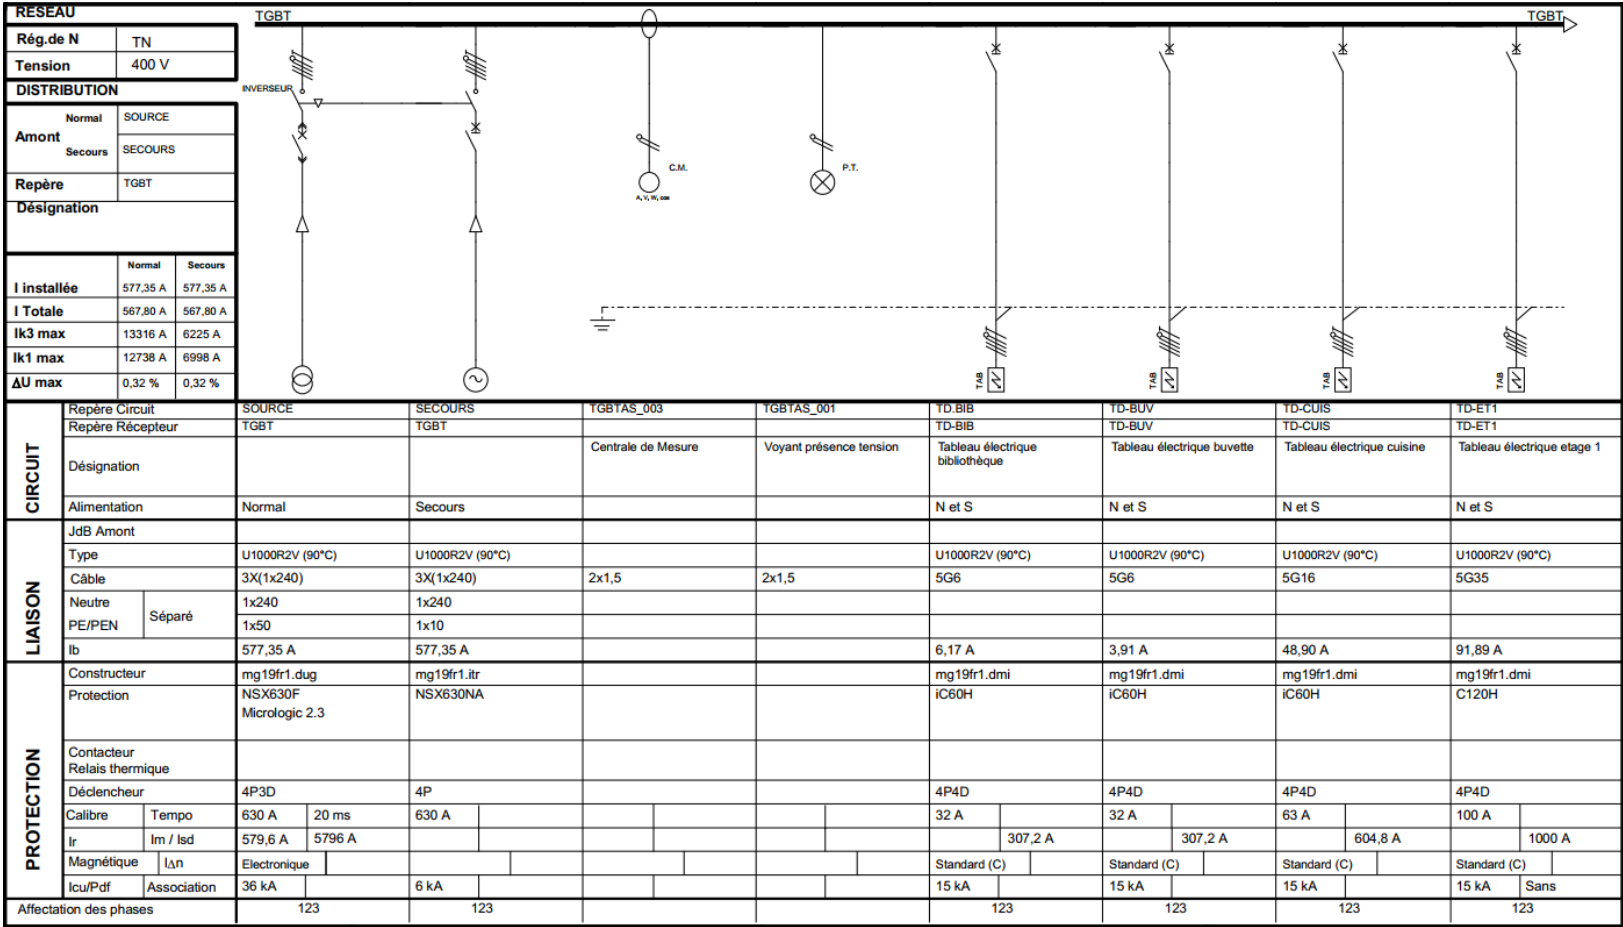


PROJET 3

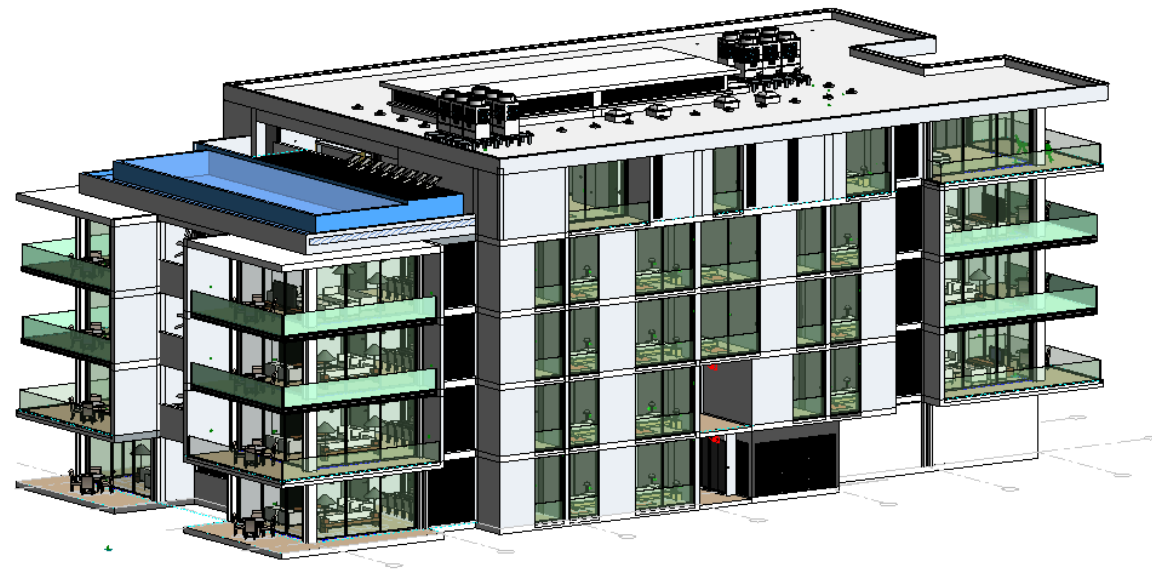


PROJECT 3

Projet d'habitation : complexe contient (deux immeuble et 7 villa avec parking. je present just un immeuble qui represente 3 étages (chaque étage contient 4 appartements) avec penthouse .


on va réalisé des installations électrique :éclairage , courant fort, et courant faible avec une note de calcul basse tension .

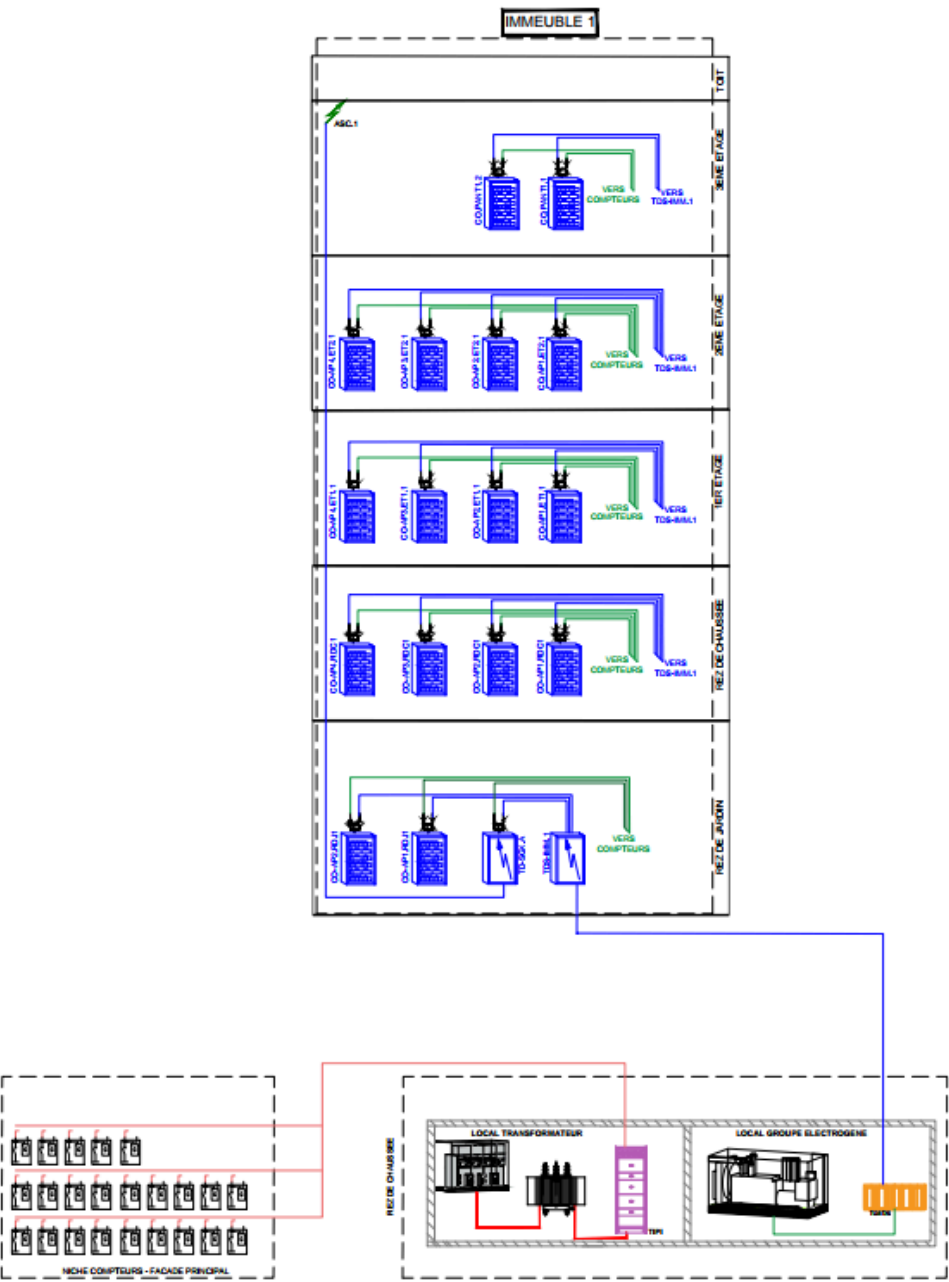


SYNOPTIQUE COURANT FORT

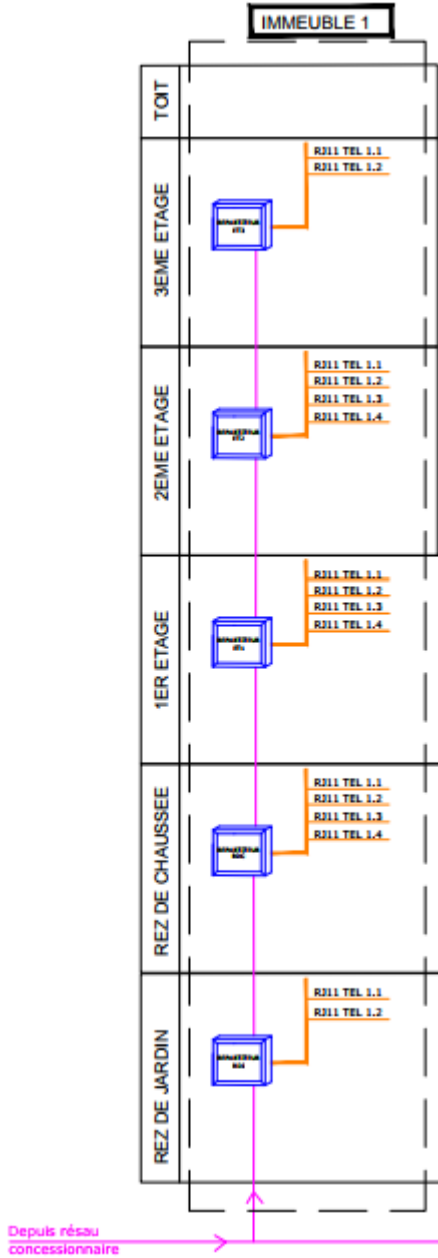


SYNOPTIQUE TELEPHONIQUE

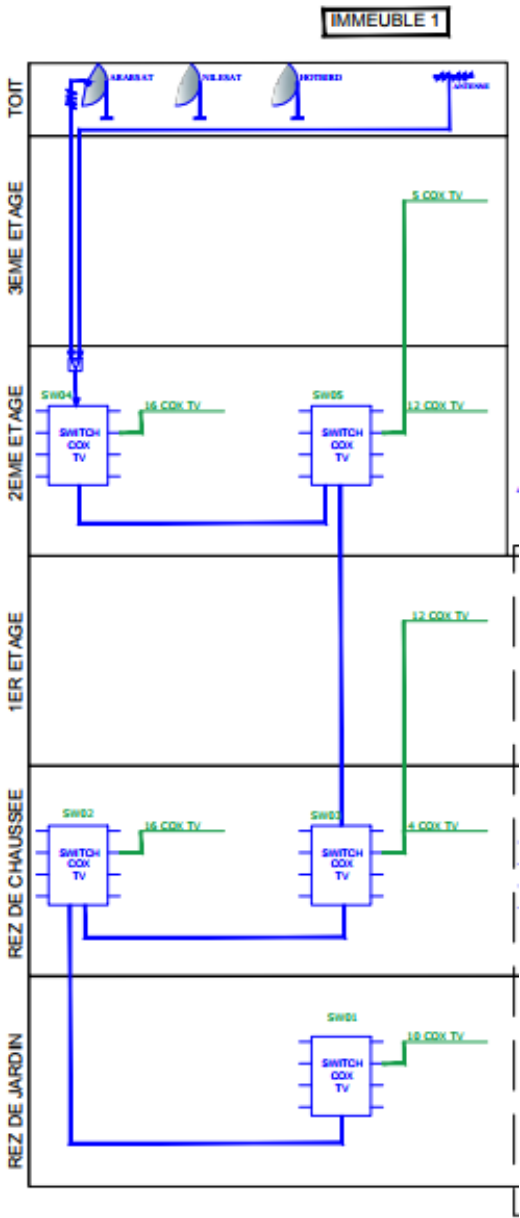


SYNOPTIQUE TV

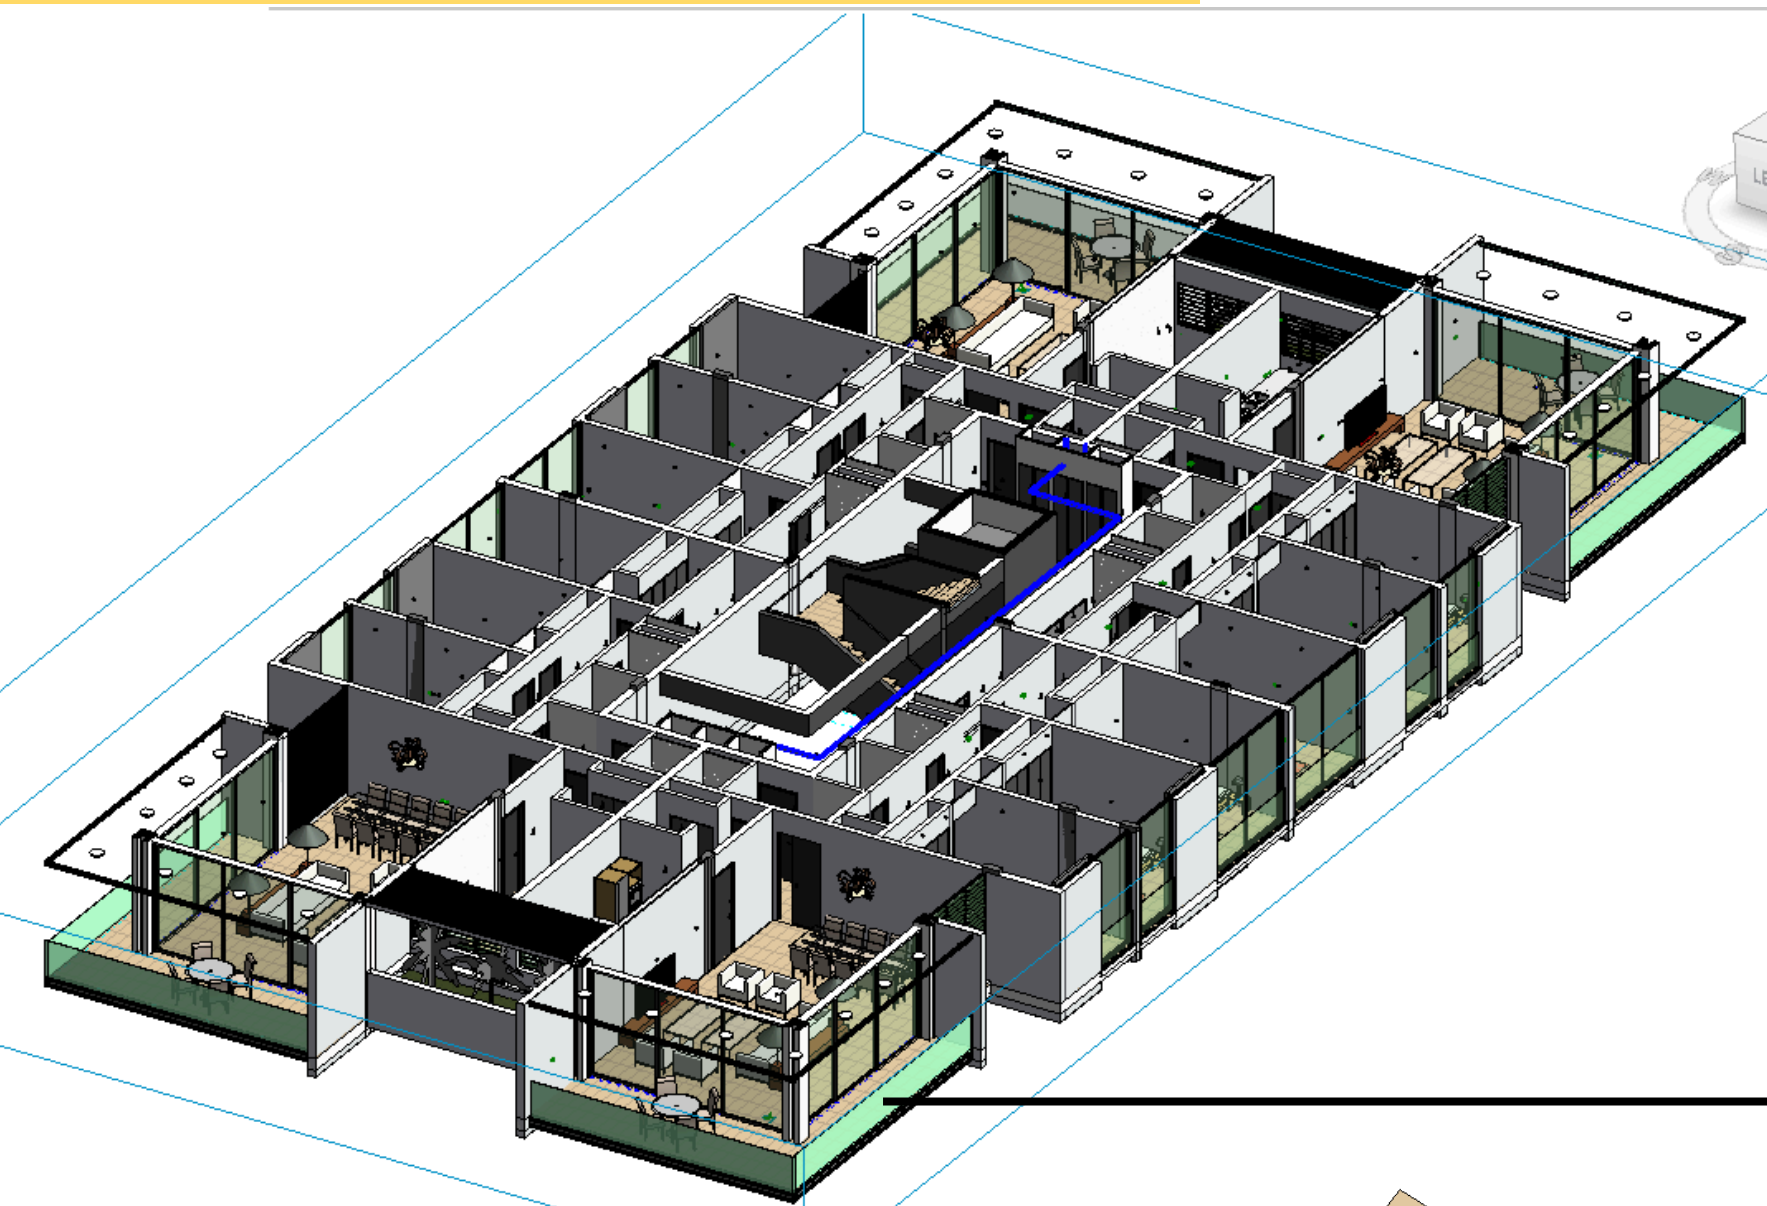



PLAN D'ETAGE

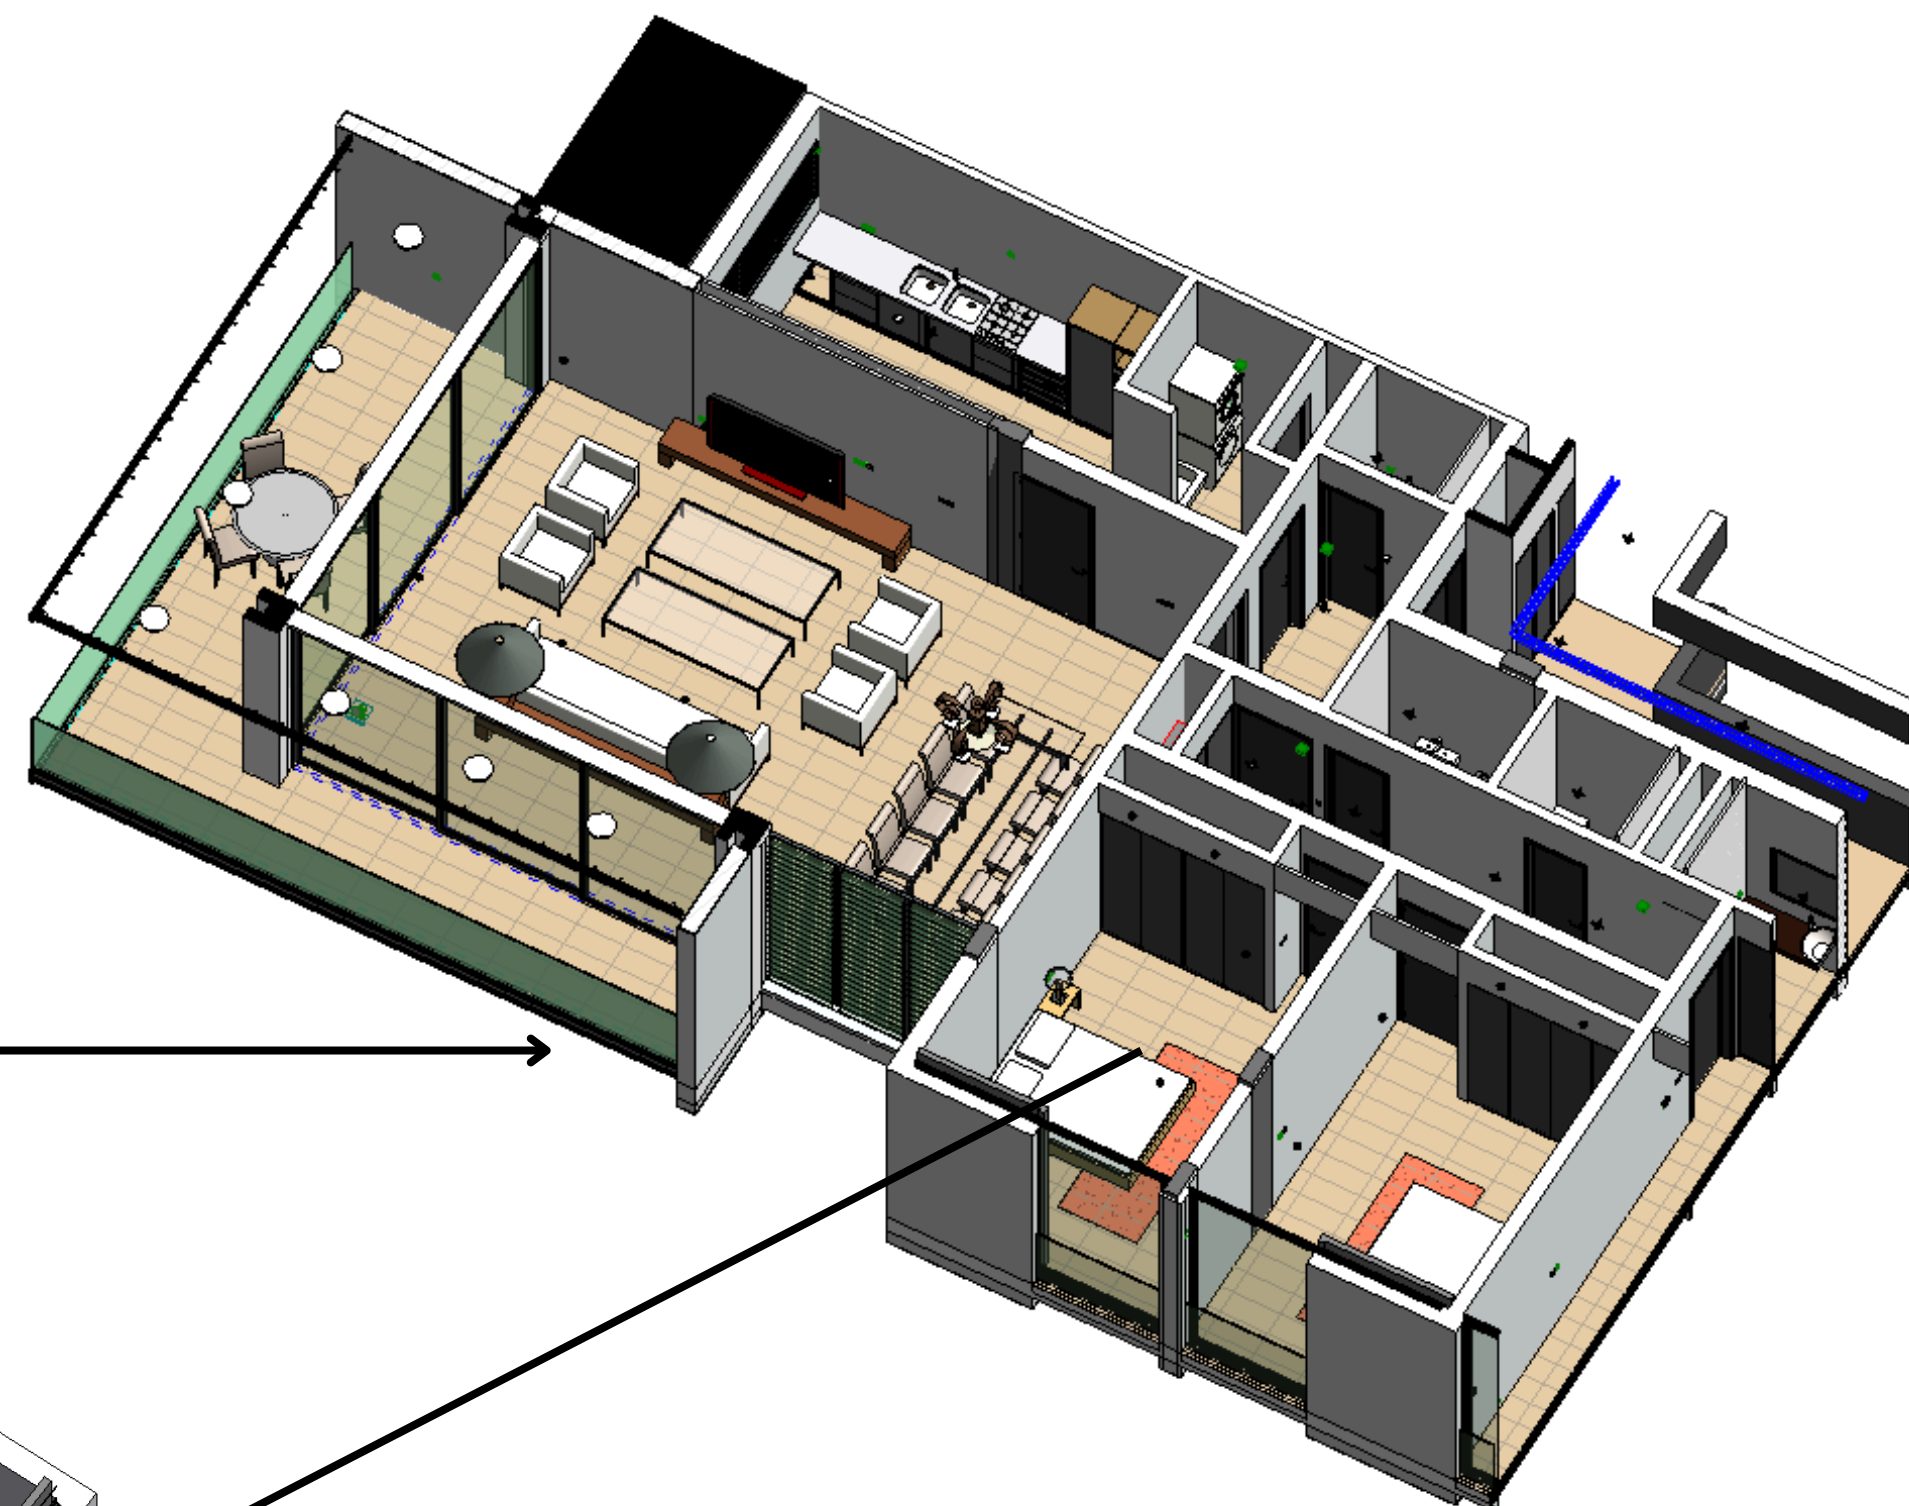


APPARTEMENT

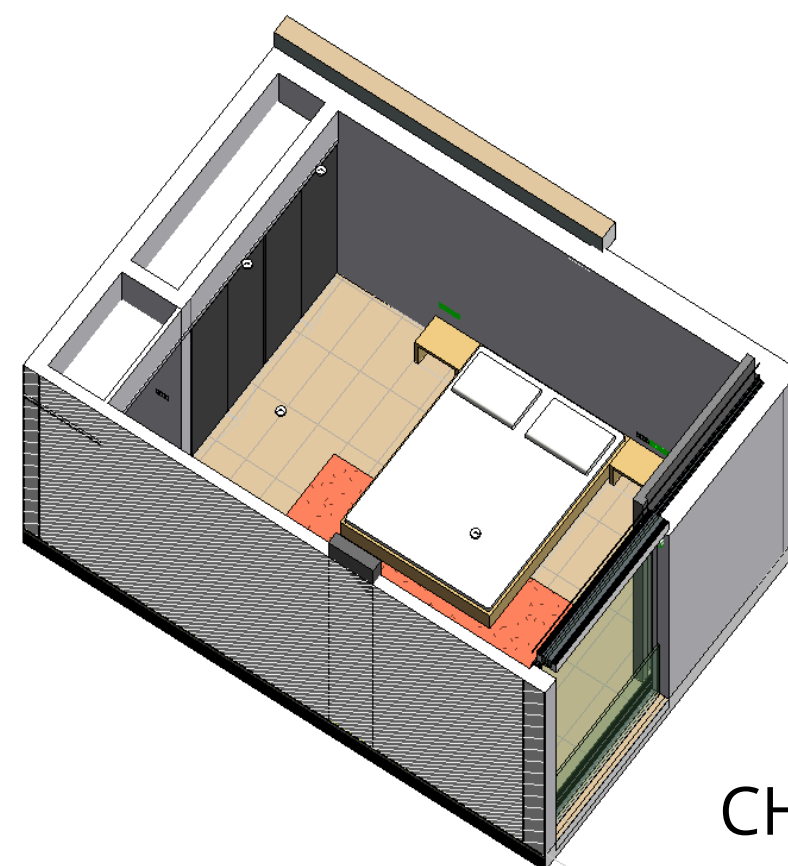

CHAMBRE

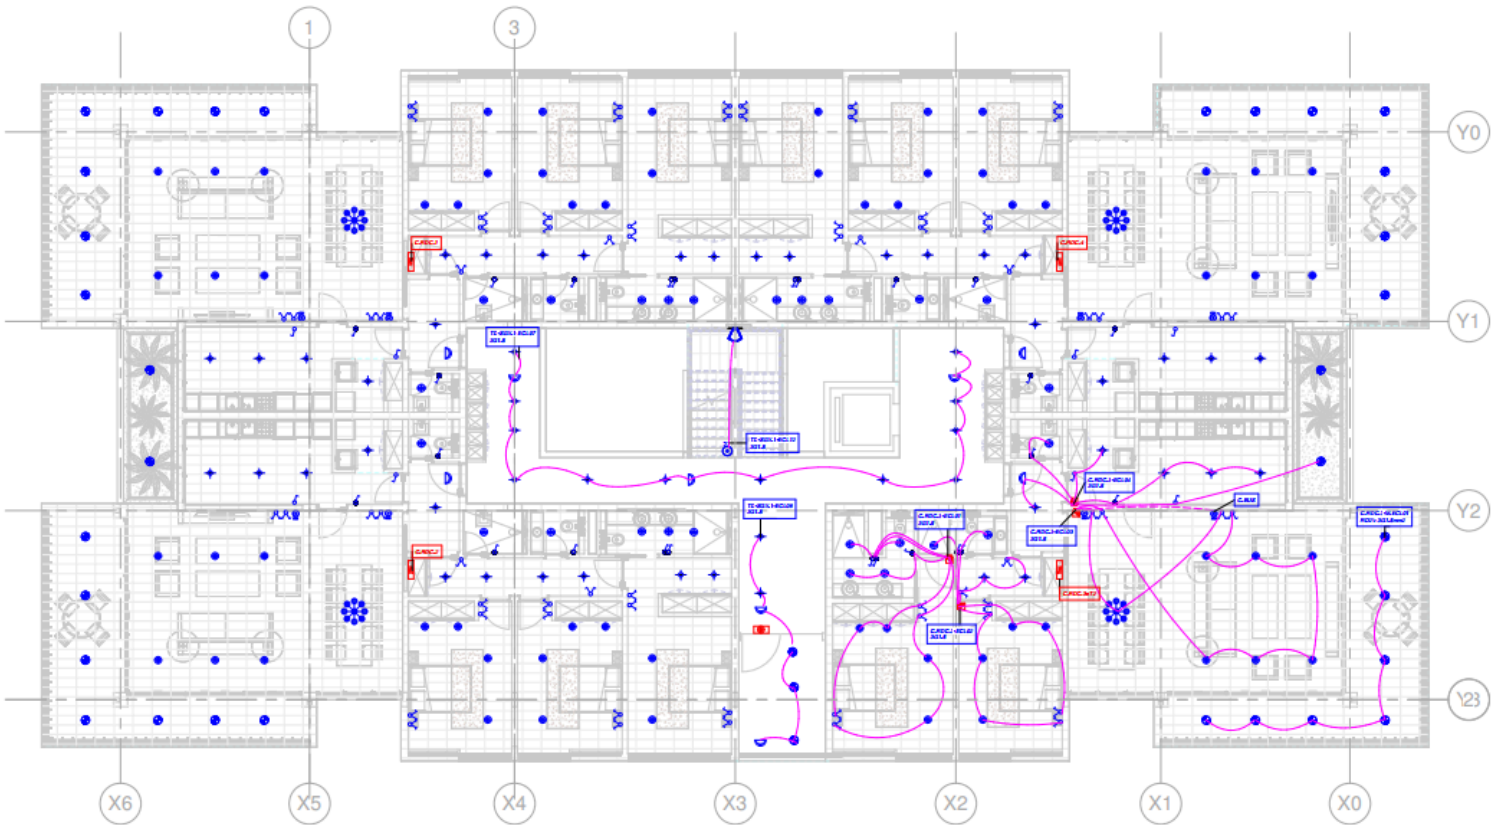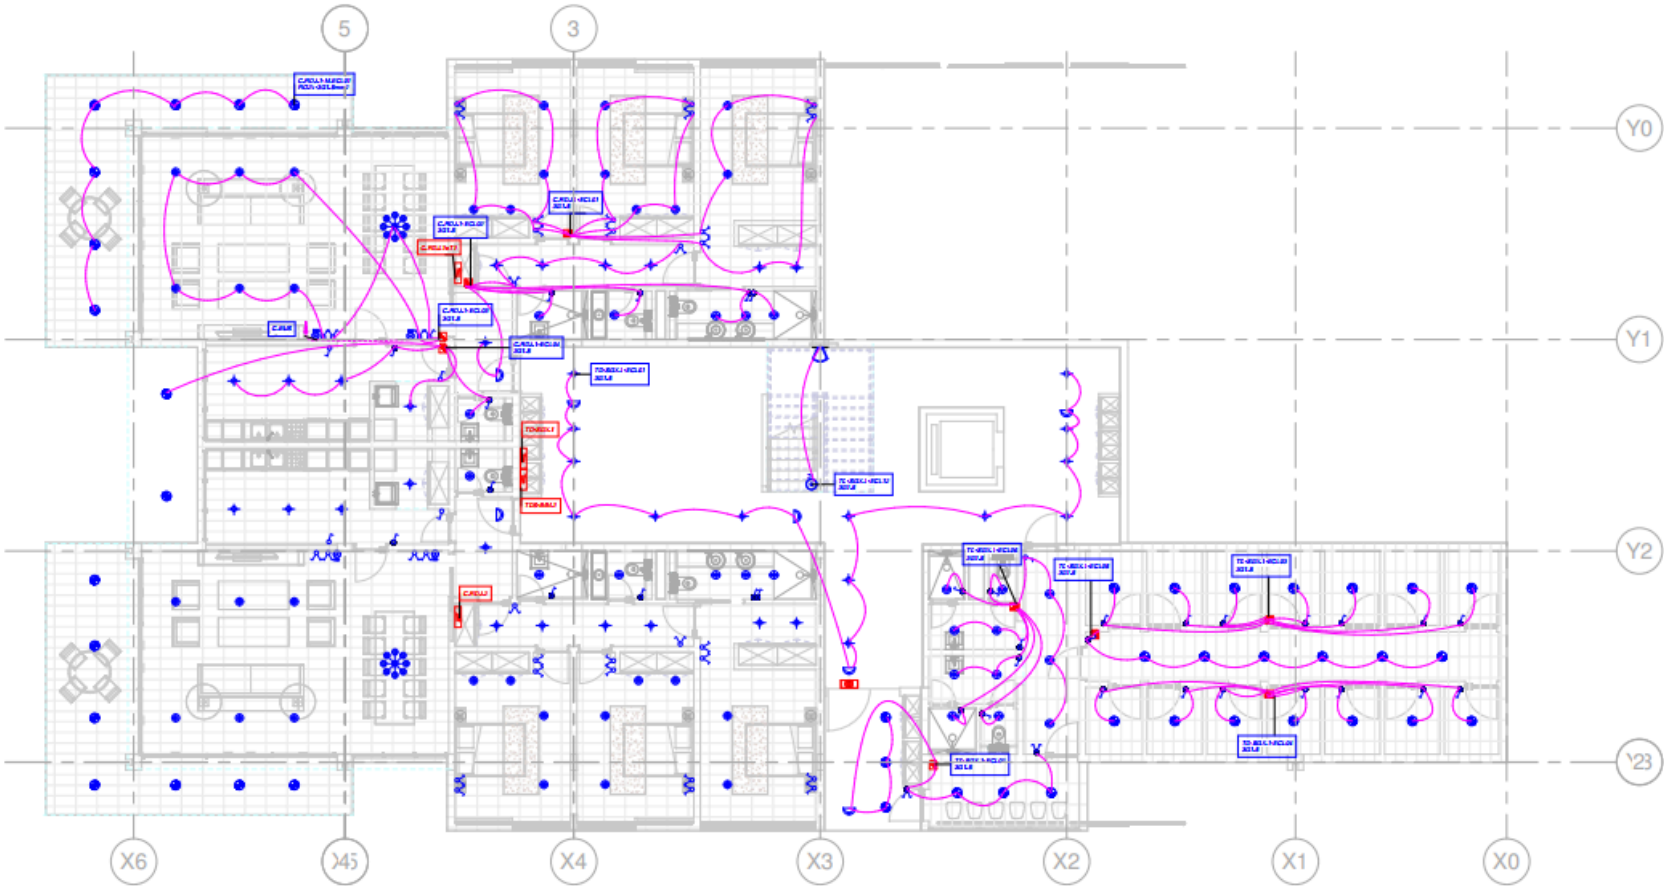



PLAN ECL RDJ

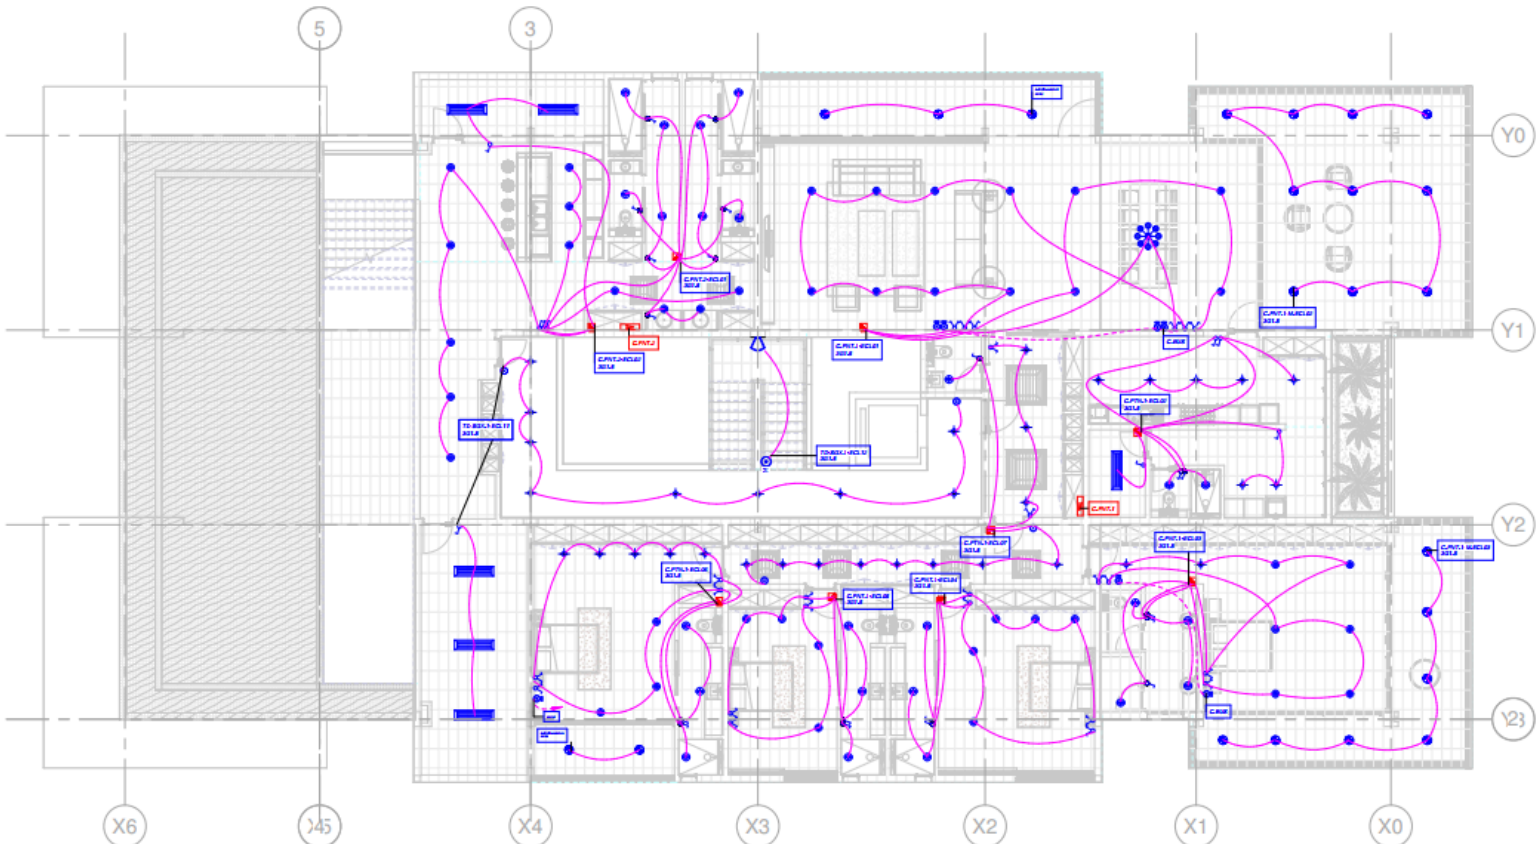


PLAN ECL PENTHOUSE

PLAN ECL RDC/ET1/ET2

LEGENDE ECLAIRAGE			
Symbole	Désignation	Symbole	Désignation
	Spot Led Encastré au Dalle 9W		Applique Led -25w
	Spot Led Encastré au Plafond 9W		Applique Etanche IP65-25w
	Spot Led Encastré IP55-9W/12V		Detecteur de Mouvement
	Lustre Avec Des Lampes Led 34W		Bouton Poussoir
	Luminaire Suspendu 20W/12V		Bouton Poussoir-KNX
	Luminaire Led Etanche IP65 1200mm-25w		Interrupteur Simple Allumage
	projecteur au sol IP 66, IK 10 corps en aluminium-12w		Interrupteur Va et Vient
	Applique Led Decoratifs 25w		Interrupteur Simple Allumage Etanche
	Lampadaires avec 2 Boule Lampe Extérieur 25w		Interrupteur Va et Vient Etanche
	Dalle Carré Led 36W		Bloc Autonomes 60 Lumens
	Spot Led Encastré 6W		Boite de Derivation
	Plafonier Etanche 9W		Coffret Electrique Encastré
	Ruban Led		

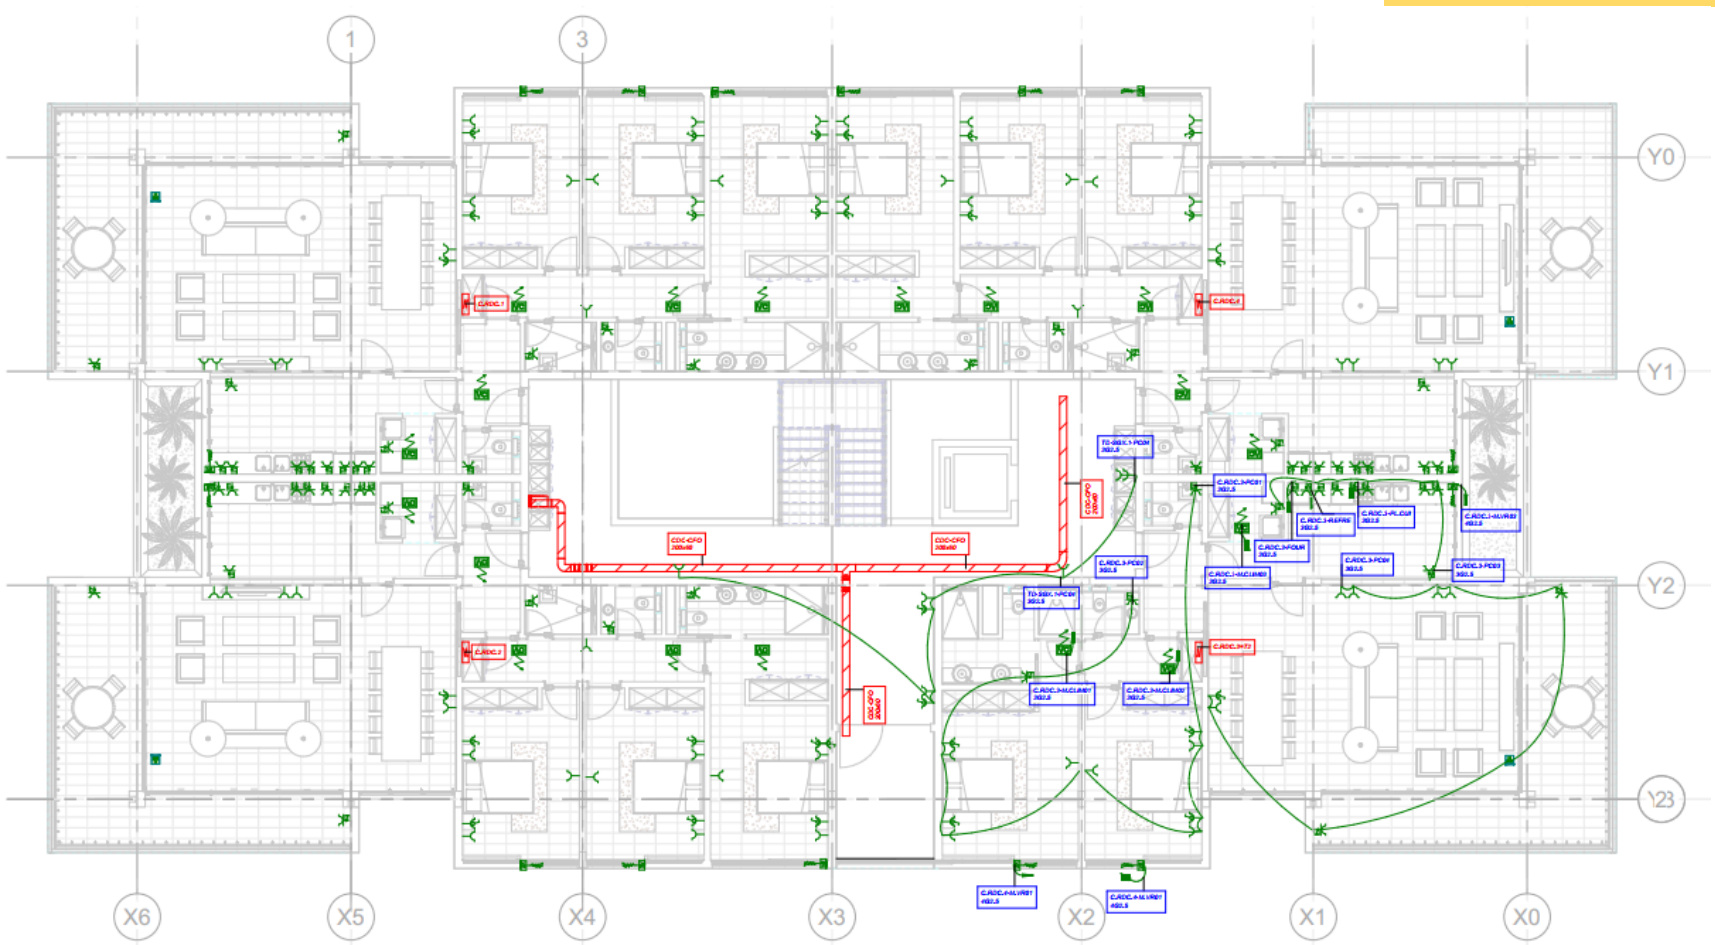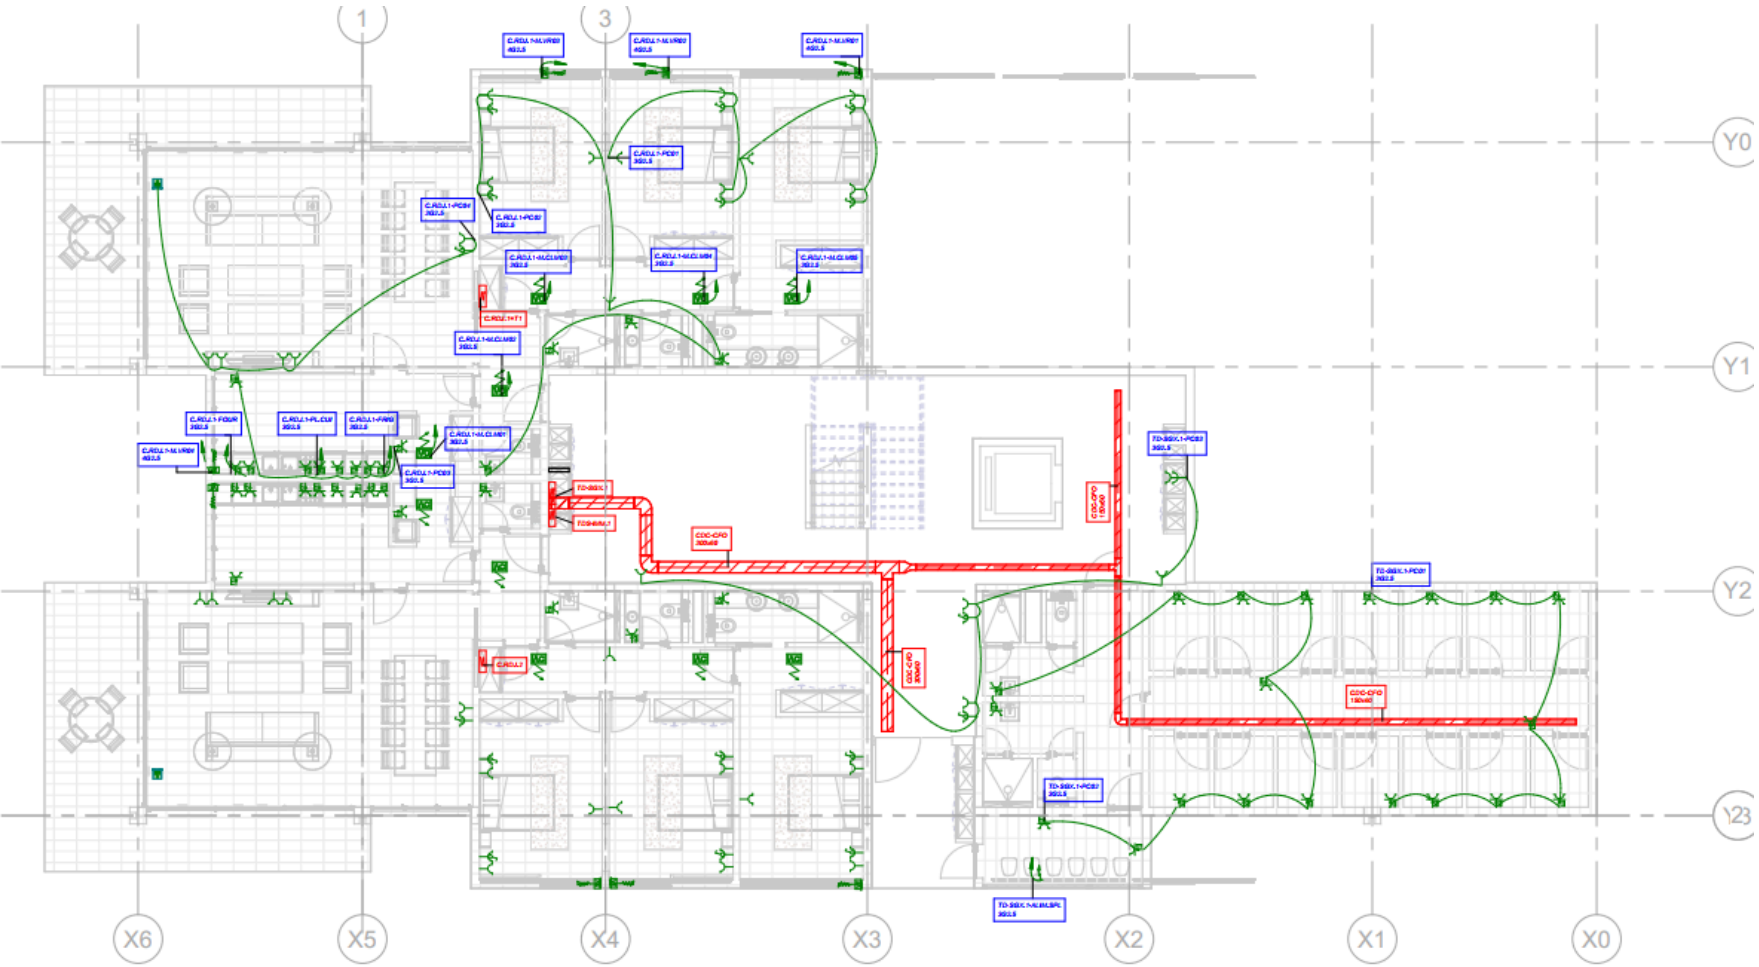

PLAN CFO RDJ

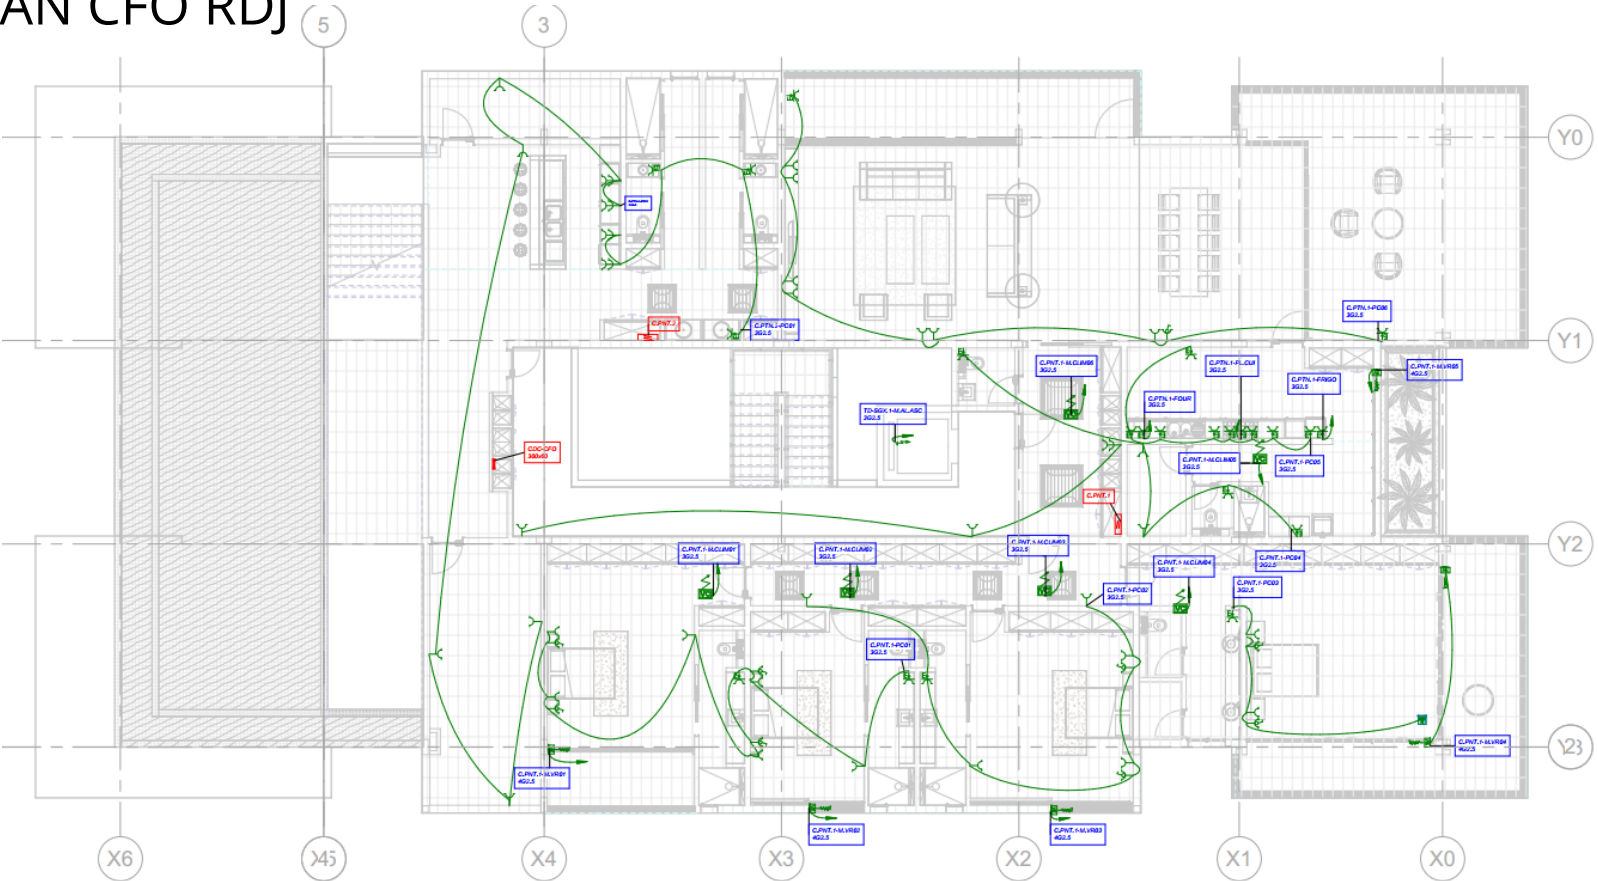


PLAN CFO RDC/ET1/ET2


LEGENDE PRISE COURANT -PCA-			
Symbole	Désignation	Symbole	Désignation
	Prise de Courant 2P+T10/16A		Réseau mise à la Terre Cuivre Nu de 35mm²
	Prise de Courant Etanche 2P+T 10/16A		Armoire Electrique
	Bloc de Deux Prises 2P+T 10/16A		Alimentation Ventilo Convecteur
	Prise Commandée par Interrupteur 2P+T10/16A		Alimentation Volet Roulant
	Boite au Sol Comprenant 3 Prises de Courant 2P+T 10/16A		Alimentation en Attente VMC
	Regard de Terre de dimension 80x80x80cm		Boite de Derivation PC

LEGENDE CHEMINS DE CABLE	
Symbole	Désignation
	Chemins de Cable CFO
	Raccord Chemins de Cable CFO
	Raccord Chemins de Cable CFO

PLAN CFO PENTHOUSE

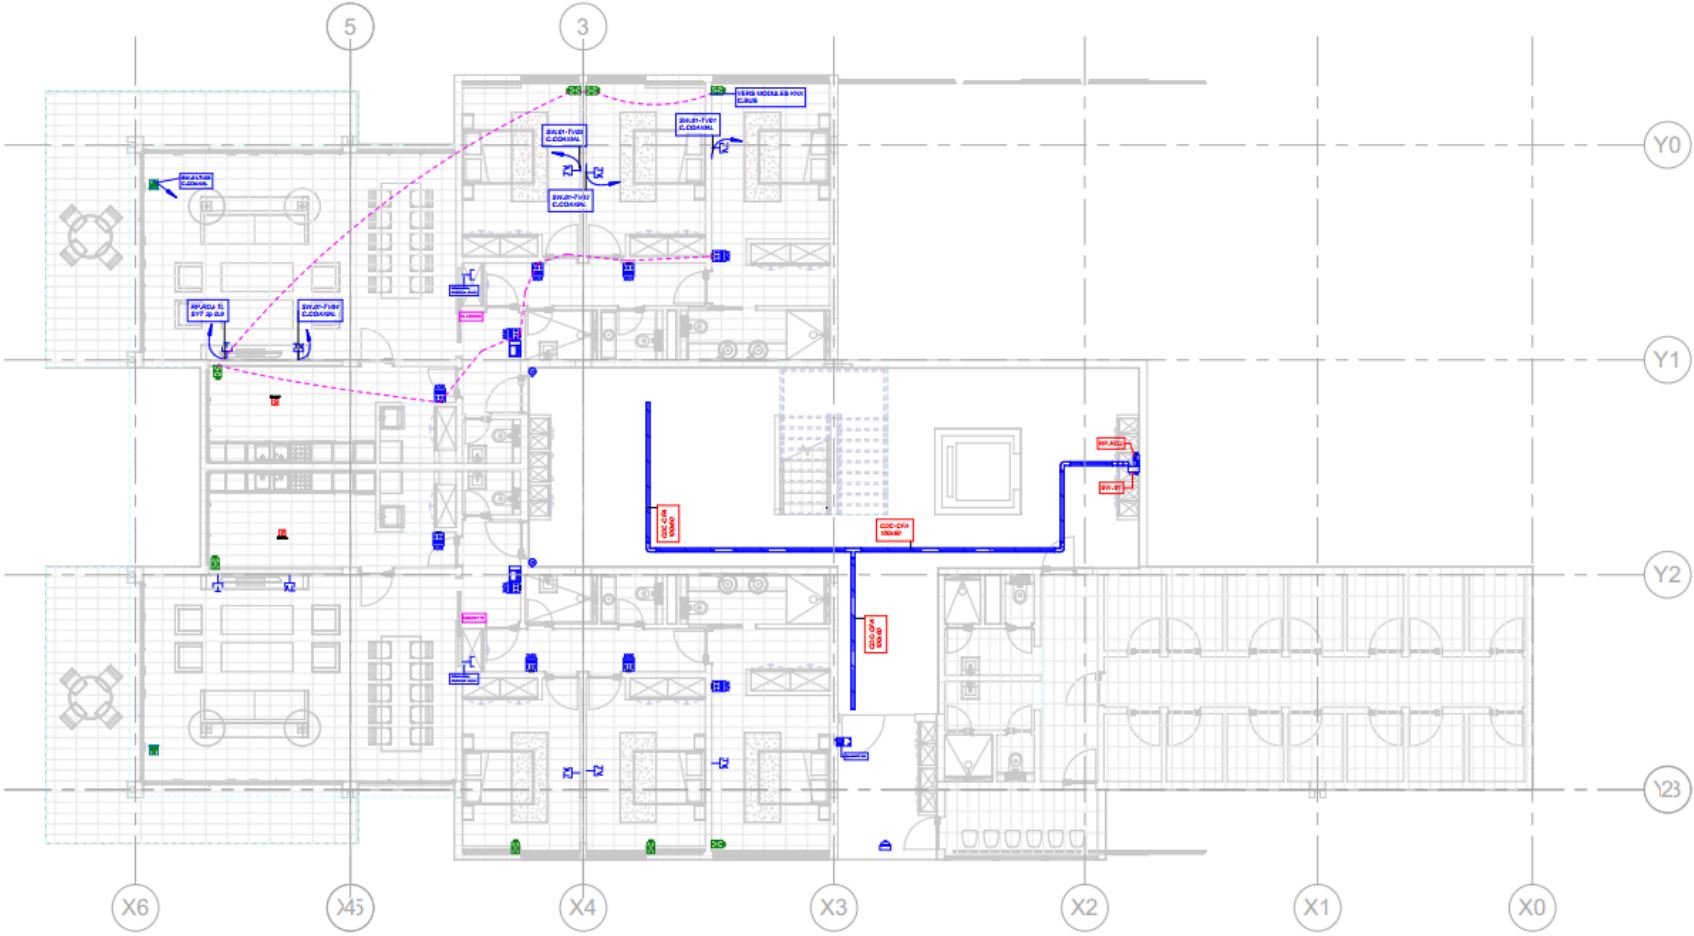

PLAN CFA RDJ

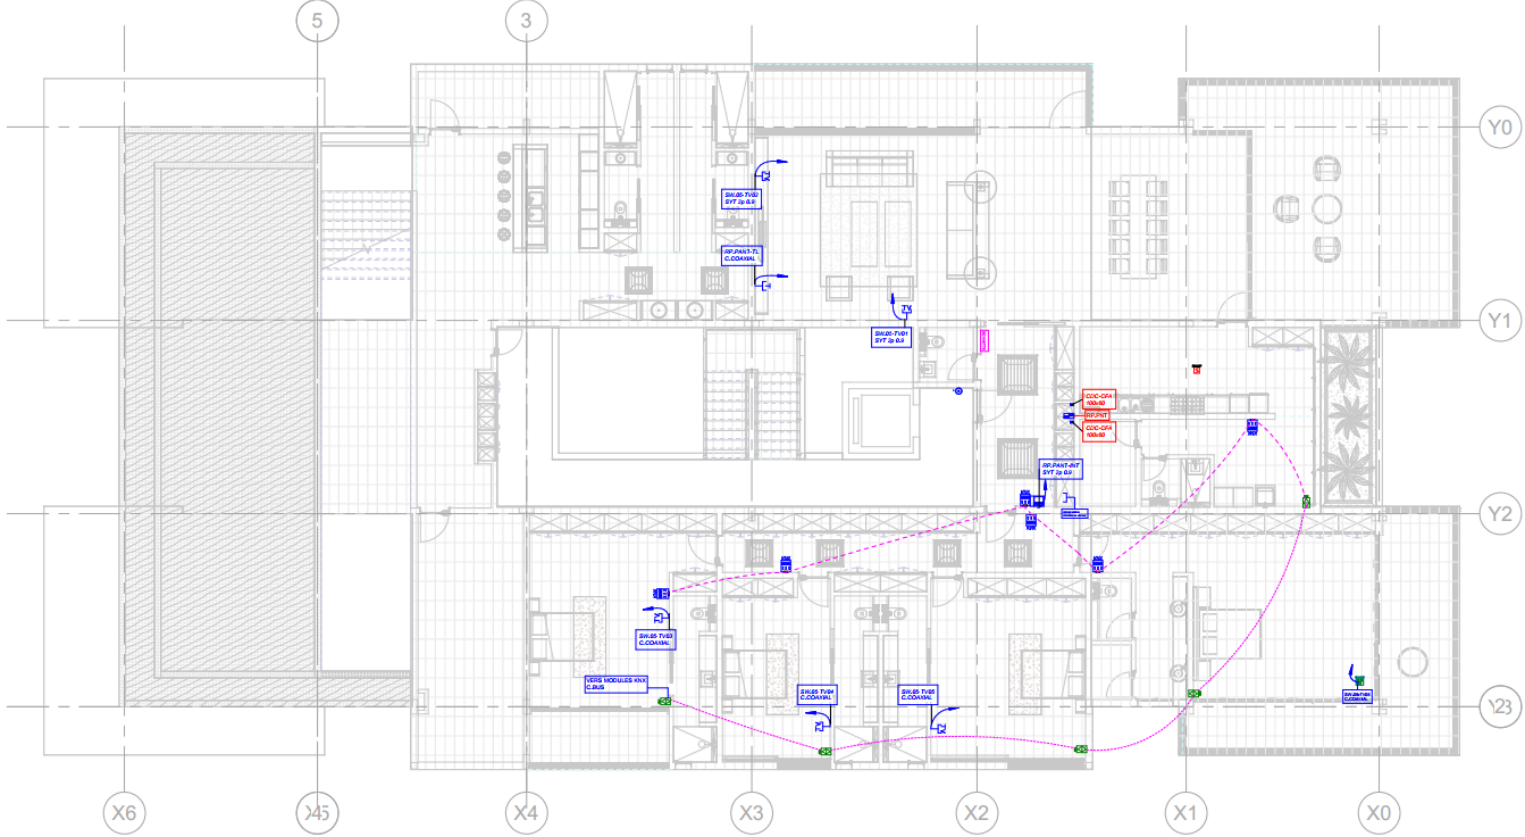

PLAN CFA RDC/ET1/ET2

PLAN CFA PENTHOUSE

LEGENDE COURANT FAIBLE -CFA-			
Symbole	Désignation	Symbole	Désignation
	Wifi		Interphone
	Prise Informatique RJ45		Bouton Sonnette
	Prise Telefonique RJ11		Sonnette
	Prise TV		Thermostat-KNX
	Boite au Sol avec 1 Prises TV		Videophone-KNX
	Armoire de Brassage Informatique		Détecteur de Fumée
	Repartiteur Telefonique		Detecteur Optique de Fumée
	Camera de Surveillance Dome		Cable Bus
	Camera de Serveillance Externe		
	Commande Volet Roulant -KNX		

LEGENDE CHEMINS DE CABLE	
Symbole	Désignation
	Chemins de Cable CFA
	Raccord Chemins de Cable CFA
	Raccord Chemins de Cable CFA

NDC APPARTEMENT 1

